

МИНИСТЕРСТВО НАУКИ И ВЫСШЕГО ОБРАЗОВАНИЯ РОССИЙСКОЙ ФЕДЕРАЦИИ
Федеральное государственное бюджетное образовательное учреждение высшего образования
Новосибирский государственный университет архитектуры, дизайна и искусств им. А. Д. Крячкова

Кафедра архитектуры

"Апарт-отель"
Курсовой проект


Выполнила:
Ткачук А.Ю .
гр. 21-314-1

Проверили:
Свешникова О.Б.
Туманик Т.Г..

Новосибирск, 2025


Ведомость чертежей

Лист	Наименование	Примечание
1	Титульник	
01	Общие данные	
2	Ведомость чертежей	
3	План на отм. +0.000	
4	План типового этажа	
5	План на отм. +4.000	
6	План на отметке -3.100 (подземная автостоянка)	
7	План на отметке -6.200	
8	Разрез 1-1	
9	Фасад в осях А-Ж	
10	Фасад в осях 1-7	

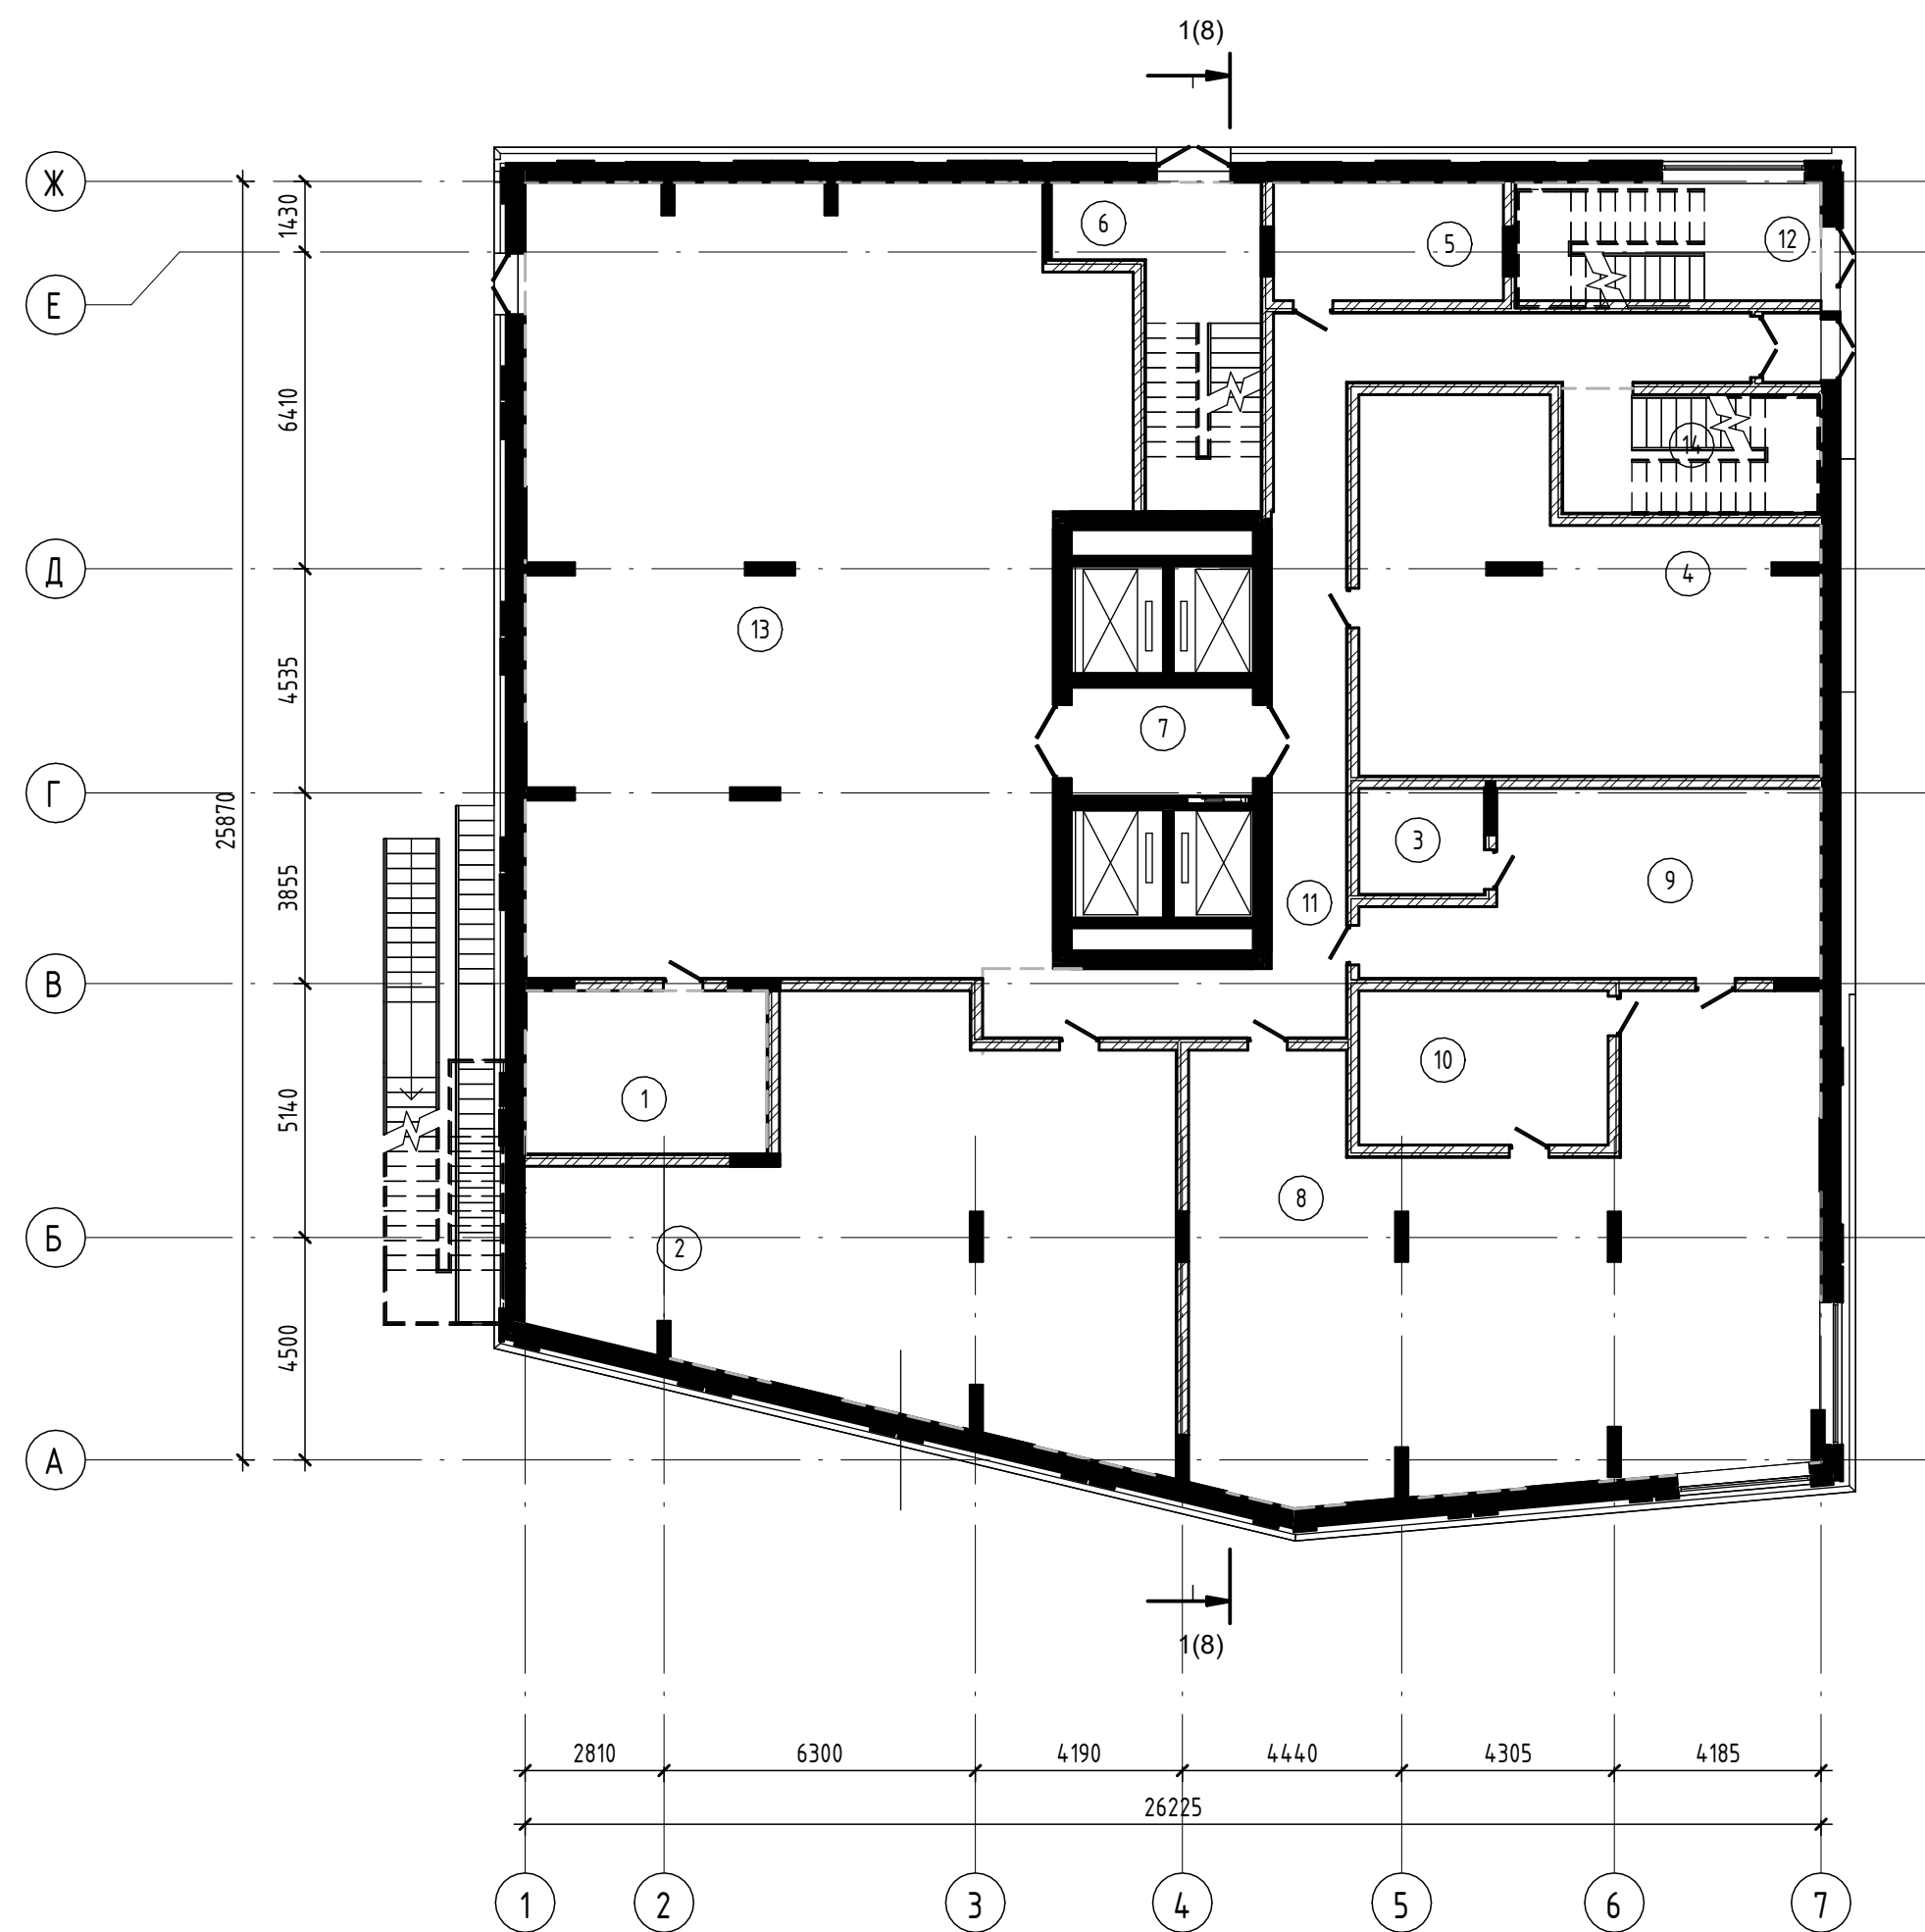

Номер помещения	Наименование	Площадь, м²	Кат. помещения
Офисные помещения			
2	Офисное помещение	86,39	
4	ТСЖ	57,15	
ПОП			
1	Комната для курения	16,47	
5	ПУИ	11,15	
6	ЛК	18,57	
7	Лифтовой холл	8,12	
11	Коридор	41,96	
12	ЛК	14,80	
13	Лобби	178,87	
14	ЛК	12,71	
Помещения общественного питания			
3	С/у	34,95	
8	Зал общественного питания	105,08	
10	С/у	15,75	


						21-414-1 АР.ГЧ			
						Апарт-отель, г. Хабаровск			
Изм.	Кол. уч.	Лист	№ док.	Подпись	Дата	Апарт-отель	Стадия	Лист	Листов
Разработала	Ткачук А.Ю.						П	3	8
Проверили	Свешникова О.Б.								
	Туманик Т.Г								
						План на 0тм. +0.000	НГУАДИ		

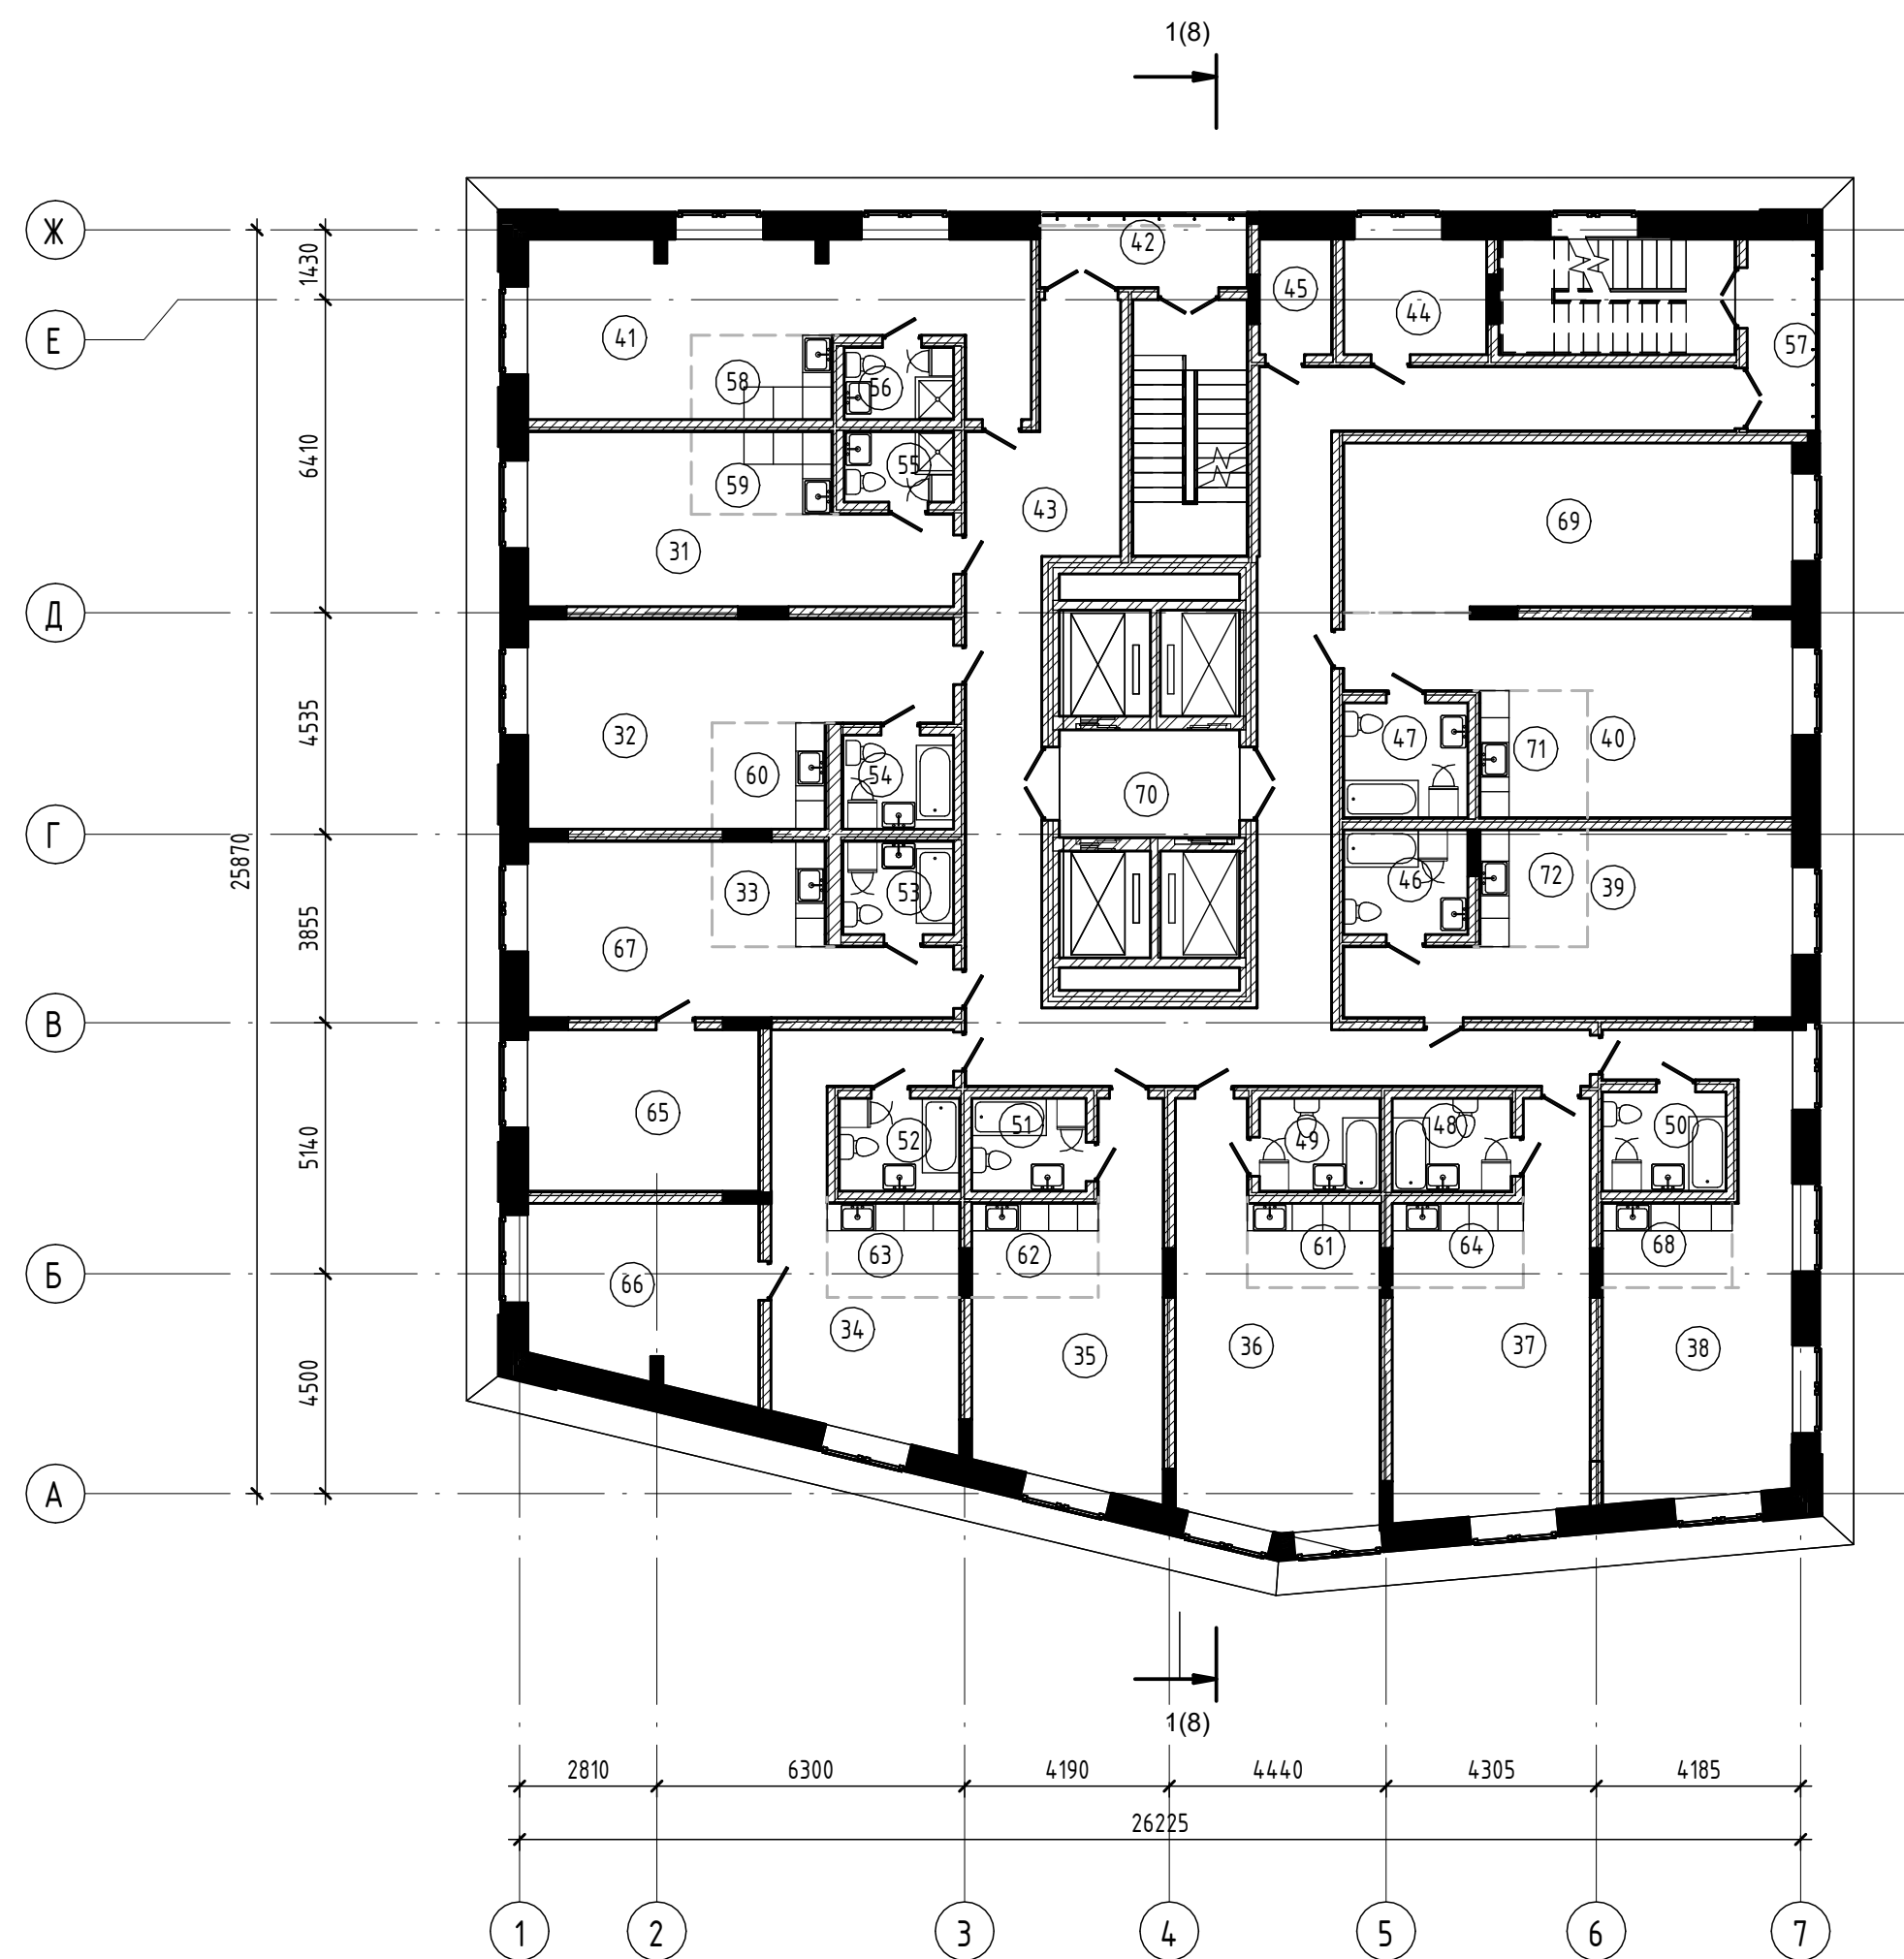

Номер помещения	Наименование	Площадь, м²	Кат. помещения
1			
41	Комната	28,13	
56	С/у	3,30	
58	Кухня-ниша	4,97	
2			
31	Комната	22,14	
55	С/у	3,23	
59	Кухня-ниша	4,86	
3			
32	Комната	26,78	
54	С/у	4,36	
60	Кухня-ниша	5,03	
4			
33	Кухня-ниша	4,99	
53	С/у	4,32	
65	Комната	15,62	
67	Комната	20,78	
5			
34	Комната	20,07	
52	С/у	4,67	
63	Кухня-ниша	5,22	
66	Комната	17,01	
6			
35	Комната	20,26	
51	С/у	4,45	
62	Кухня-ниша	4,98	
7			
36	Комната	26,06	
49	С/у	4,69	
61	Кухня-ниша	4,69	
		260,61	

Номер помещения	Наименование	Площадь, м²	Кат. помещения
8			
37	Комната	24,18	
48	С/у	4,62	
64	Кухня-ниша	4,63	
9			
38	Комната	25,62	
50	С/у	5,14	
68	Кухня-ниша	4,58	
10			
39	Комната	23,37	
46	С/у	5,44	
72	Кухня-ниша	5,26	
11			
40	Комната	24,74	
47	С/у	5,97	
69	Комната	31,09	
71	Кухня-ниша	5,72	
		170,37	
ПОП			
42	Лоджия	5,64	
43	Коридор	75,64	
44	Зона МГН	6,92	
45	ПУИ	3,50	
57	Лоджия	5,79	
70	Лифтовой холл	8,12	
		105,60	

						21-414-1 АР.ГЧ			
						Апарт-отель, г. Хабаровск			
Изм.	Кол. уч.	Лист	№ док.	Подпись	Дата	Апарт-отель	Стадия	Лист	Листов
Разработала	Ткачук А.Ю.						П	4	8
Проверили	Свешникова О.Б.								
		Туманик Т.Г				План типового этажа	НГУАДИ		

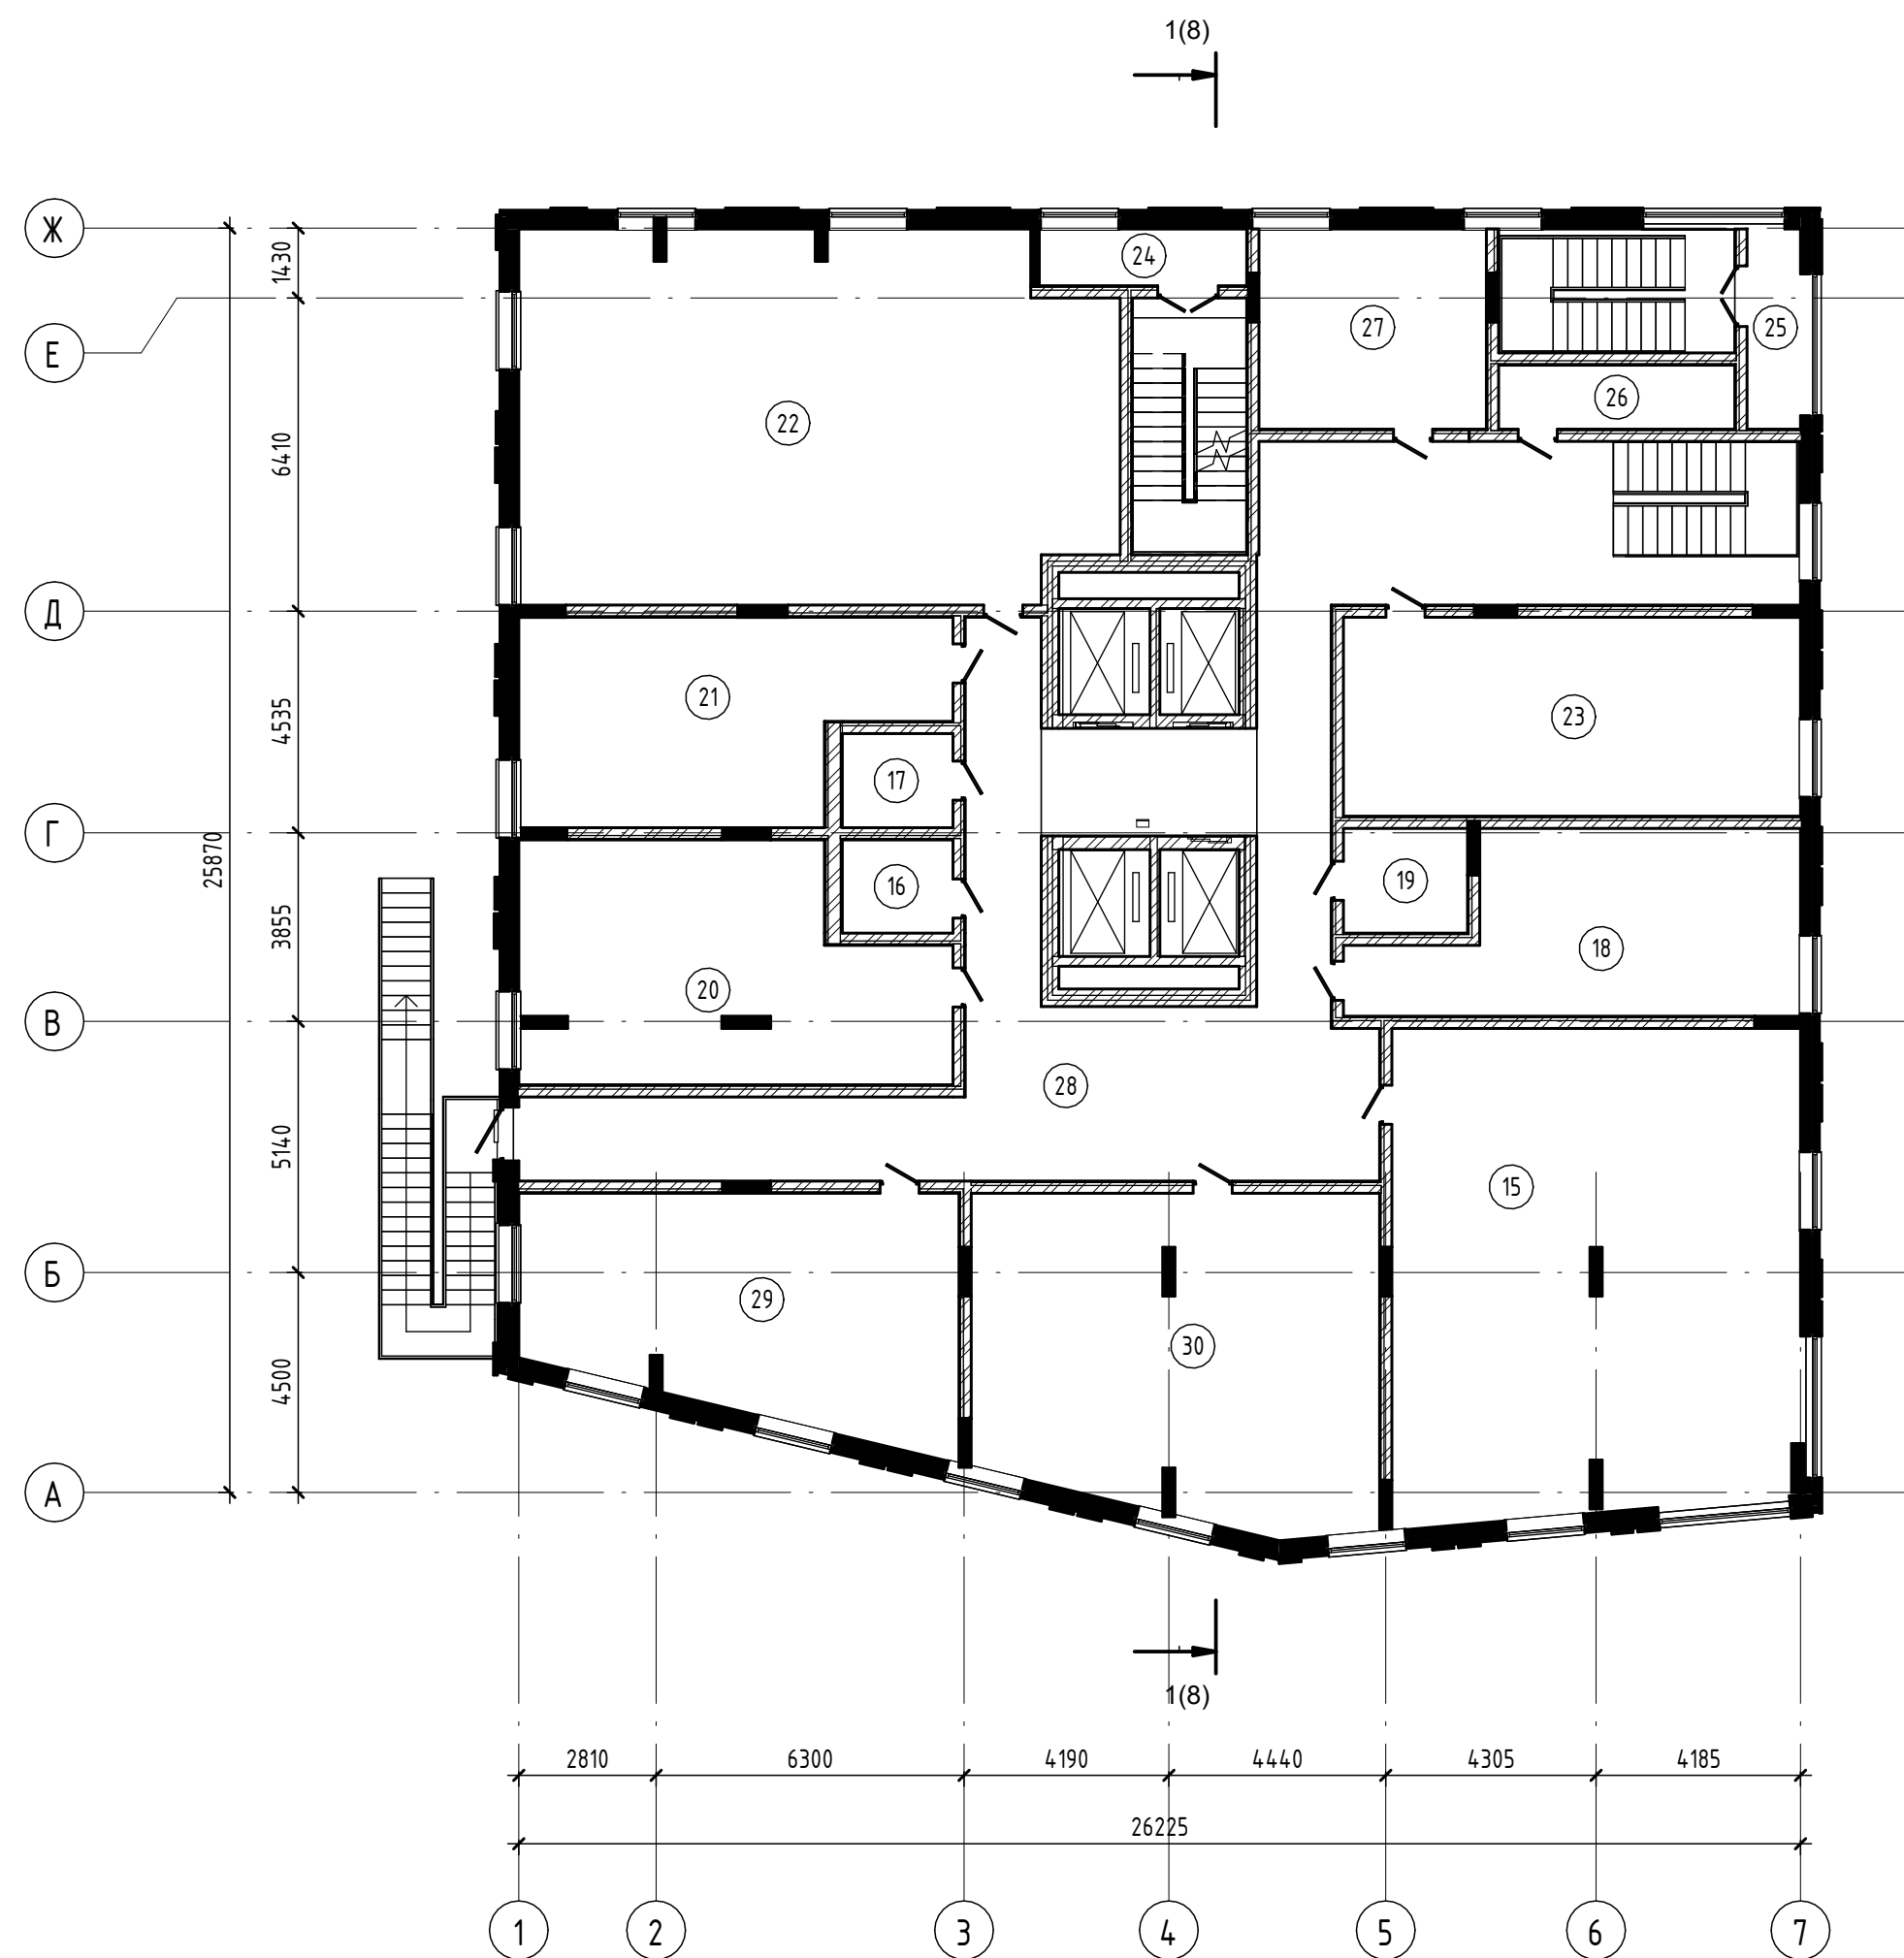

Номер помещения	Наименование	Площадь, м²	Кат. помещения
-----------------	--------------	-------------	----------------

Офисные помещения

15	Офисное помещение	82,17	
18	Офисное помещение	29,26	
20	Офисное помещение	38,33	
21	Офисное помещение	32,52	
22	Офисное помещение	90,09	
23	Офисное помещение	38,06	
27	Офисное помещение	19,06	
29	Офисное помещение	39,89	
30	Офисное помещение	53,95	


423,33

ПОП


16	С/у	4,32	
17	С/у	4,36	
19	С/у	5,44	
24	Лоджия	4,93	
25	Лоджия	4,48	
26	ПУИ	6,33	
28	Коридор	117,27	

147,14


							21-414-1 АР.ГЧ			
							Апарт-отель, г. Хабаровск			
Изм.	Кол. уч.	Лист	№ док.	Подпись	Дата		Апарт-отель	Стадия	Лист	Листов
Разработала		Ткачук А.Ю.						П	5	8
Проверили		Свешникова О.Б.								
		Туманик Т.Г.					План на отм. +4.000	НГУАДИ		

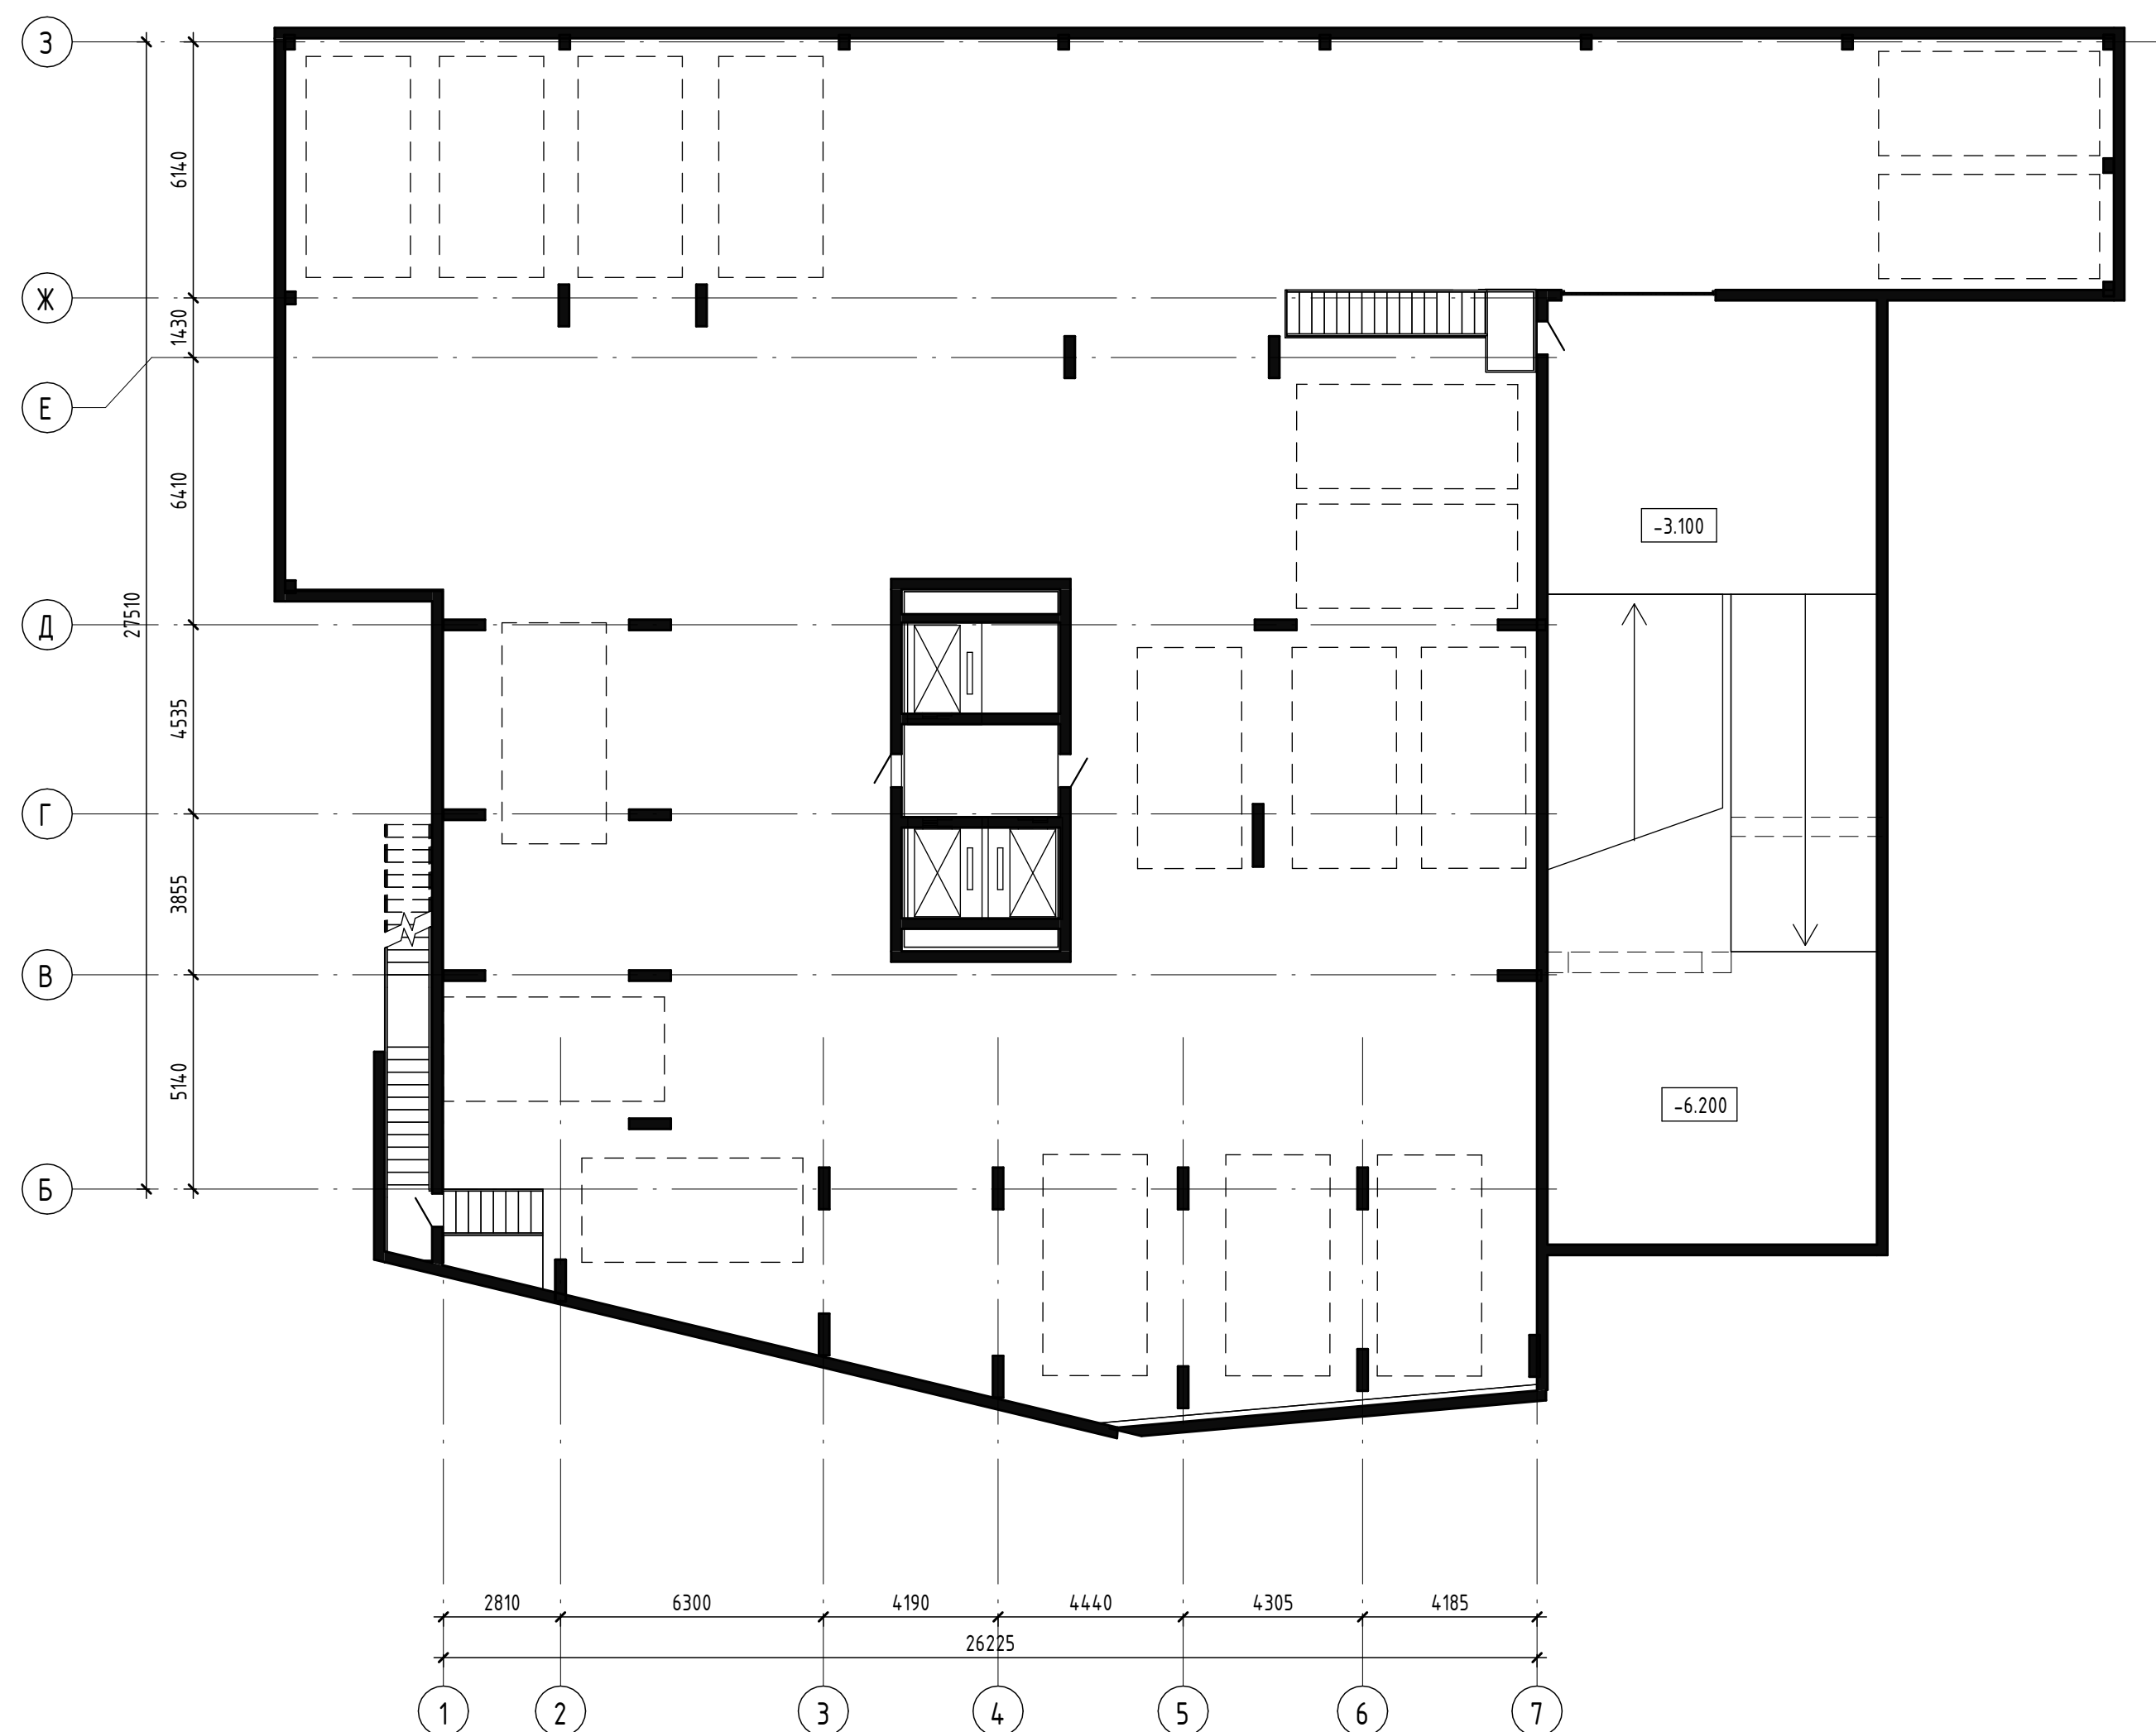

						21-414-1 АР.ГЧ			
						Апарт-отель, г. Хабаровск			
Изм.	Кол. уч.	Лист	№ док.	Подпись	Дата	Апарт-отель	Стадия	Лист	Листов
Разработала		Ткачук А.Ю.					П	6	8
Проверили		Свешникова О.Б.							
		Туманик Т.Г				План на отметке -3.100 (подземная автостоянка)	НГУАДИ		

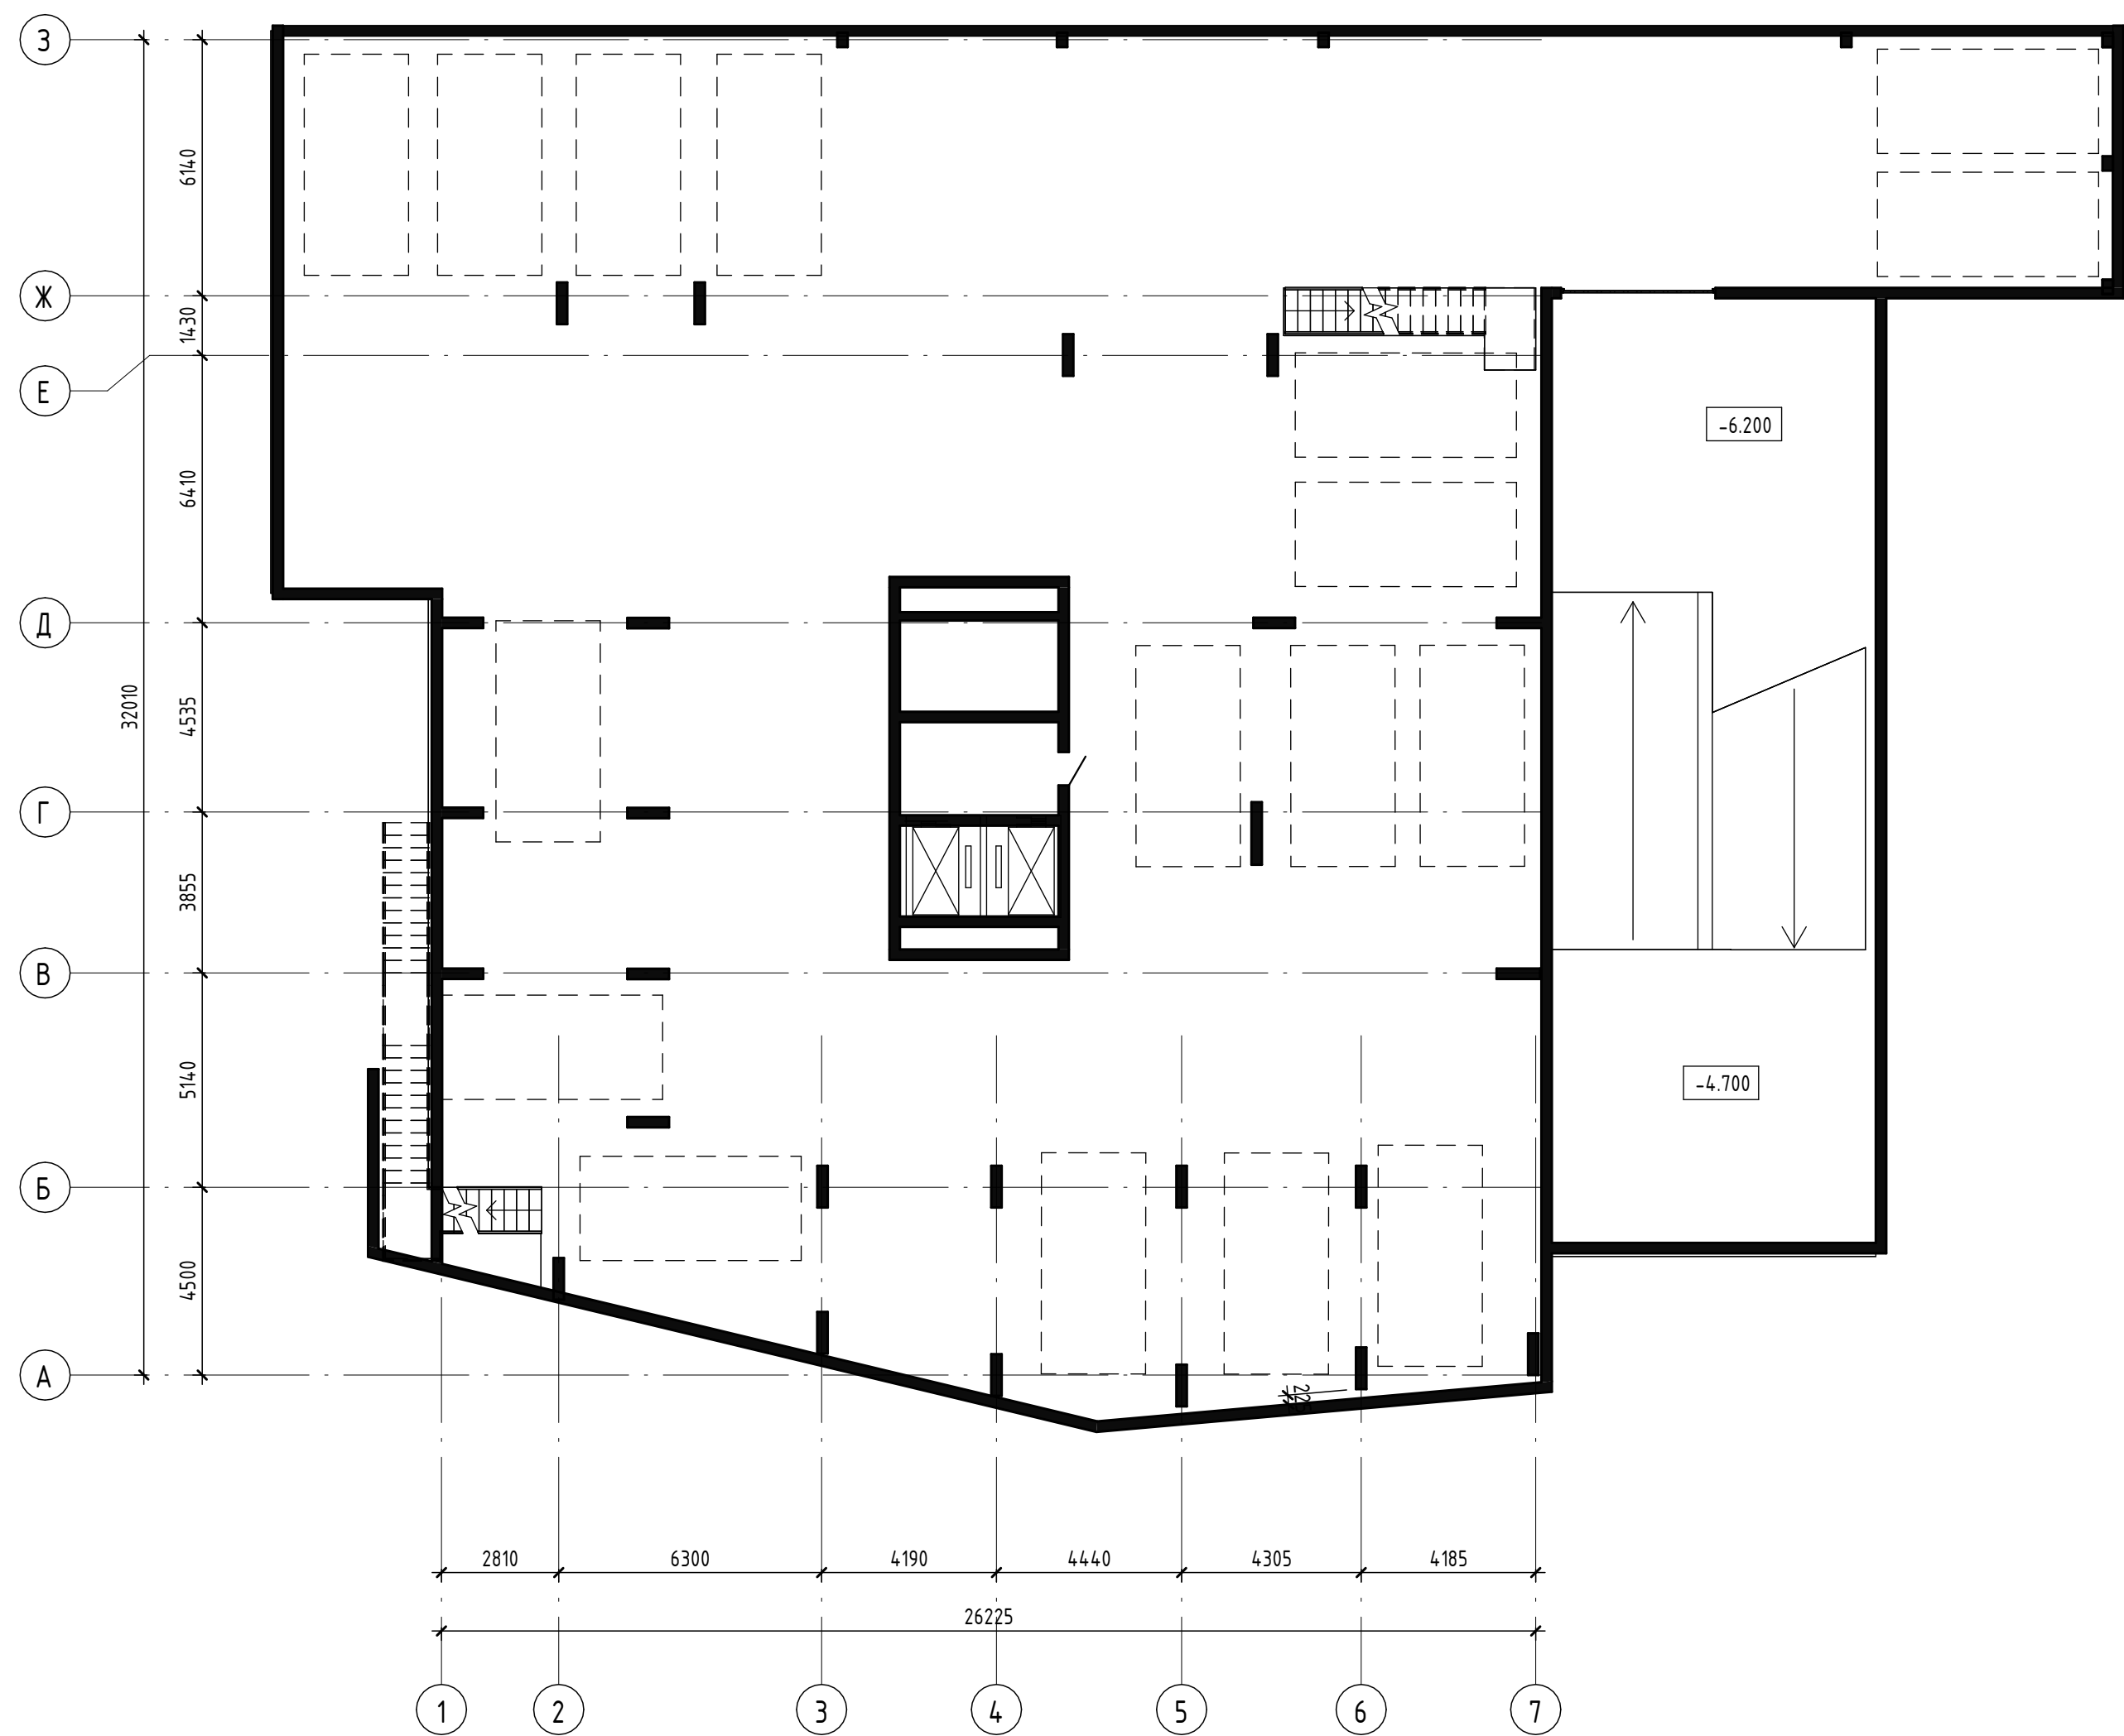

							21-414-1 АР.ГЧ			
							Апарт-отель, г. Хабаровск			
Изм.	Кол. уч.	Лист	№ док.	Подпись	Дата		Апарт-отель	Стадия	Лист	Листов
Разработала	Ткачук А.Ю.							П	7	8
Проверили	Свешникова О.Б.									
	Туманик Т.Г.						План на отметке -6.200	НГУАДИ		

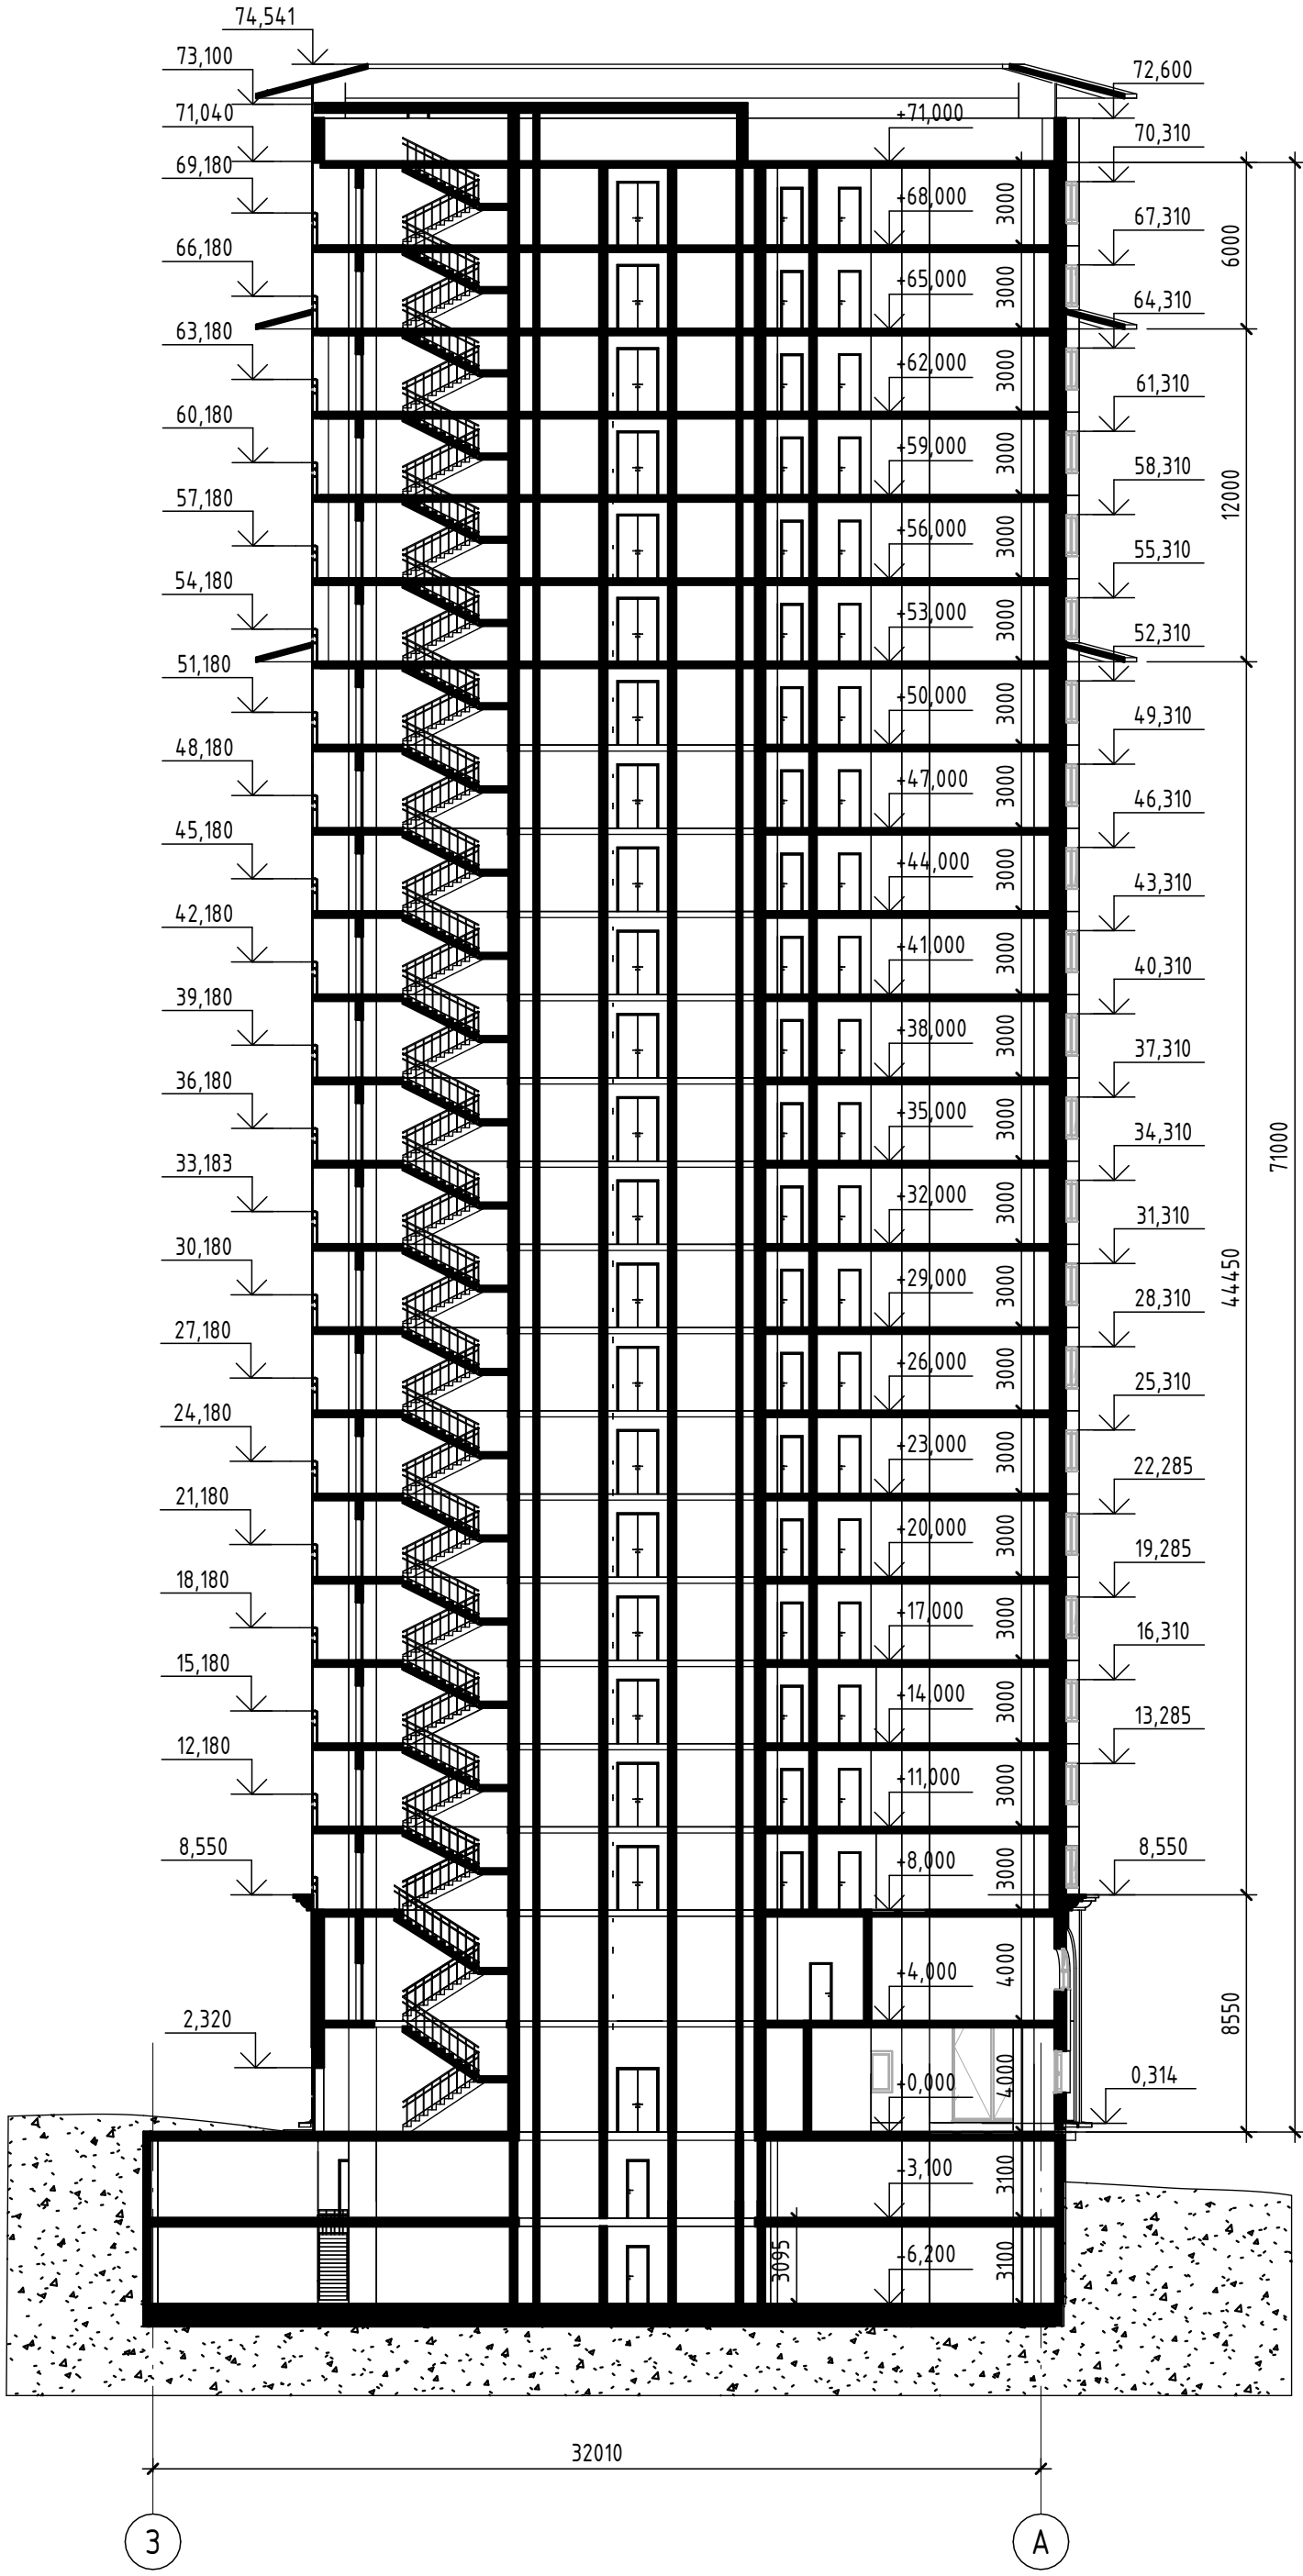

						21-414-1 АР.ГЧ			
						Апарт-отель, г. Хабаровск			
Изм.	Кол. уч.	Лист	№ док.	Подпись	Дата	Апарт-отель	Стадия	Лист	Листов
Разработала		Ткачук А.Ю.					П	8	8
Проверили		Свешникова О.Б.							
		Туманик Т.Г				Разрез 1-1	НГУАДИ		



