АВТОЗАПРАВОЧНАЯ СТАНЦИЯ

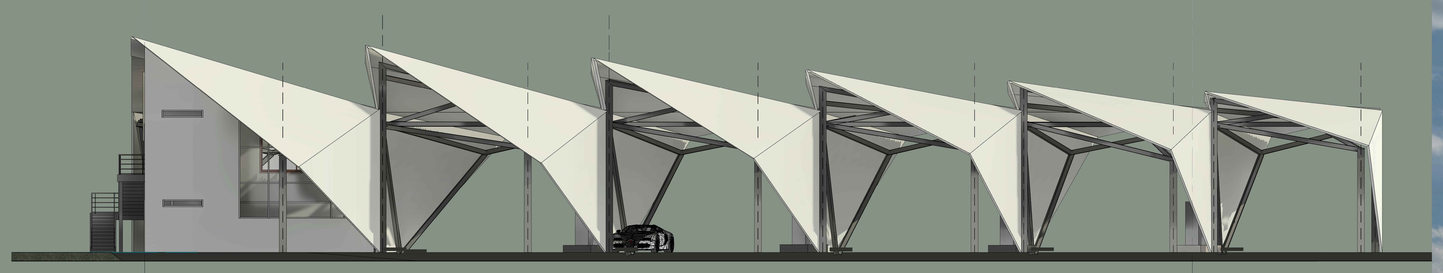

ФАСАД В ОСЯХ 1-7 М1:150

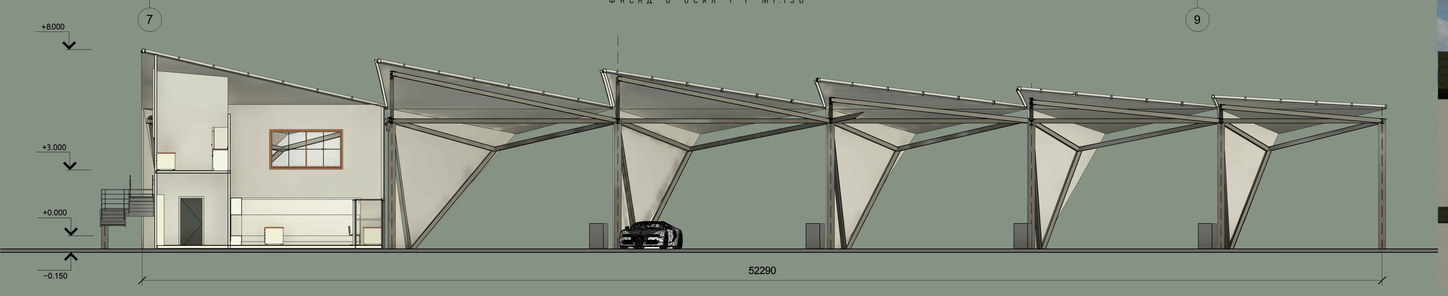

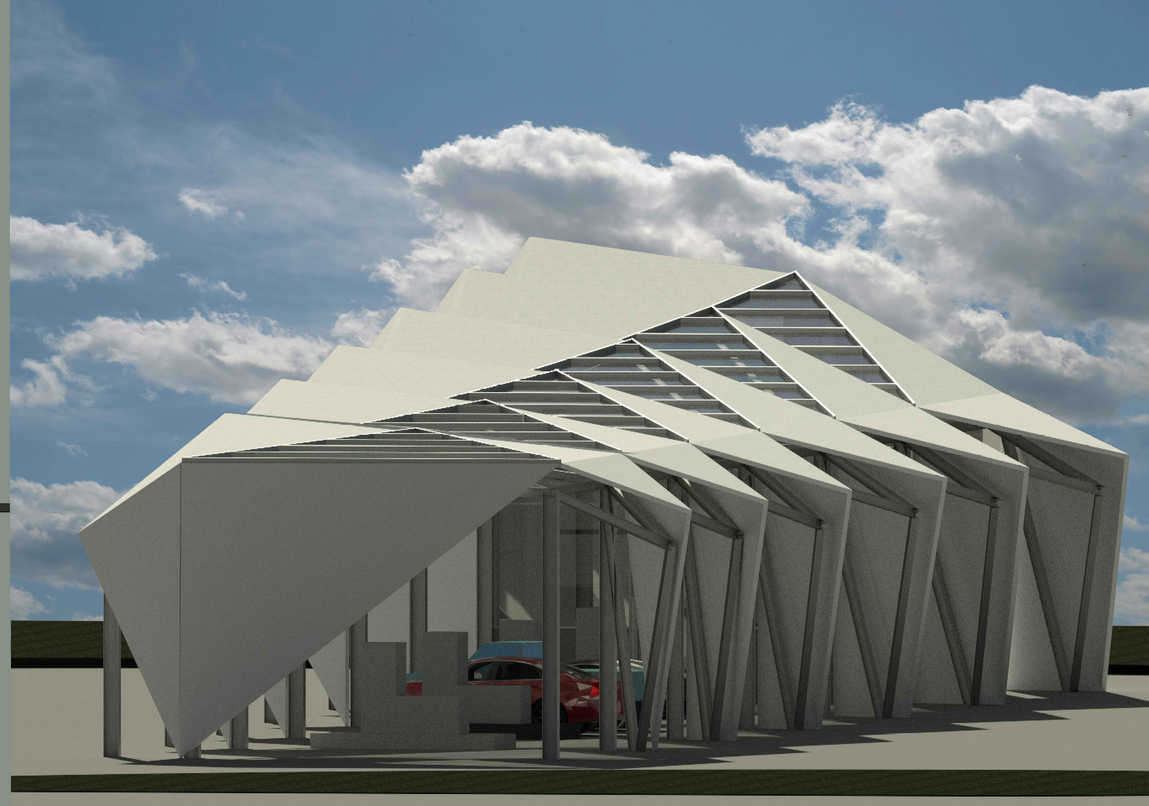

РАЗРЕЗ А-А М1:150

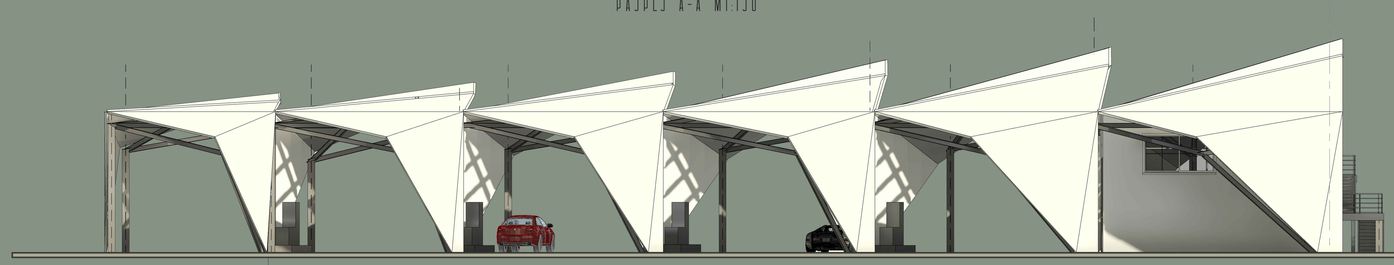

ФАСАД В ОСЯХ 7-1 М1:150

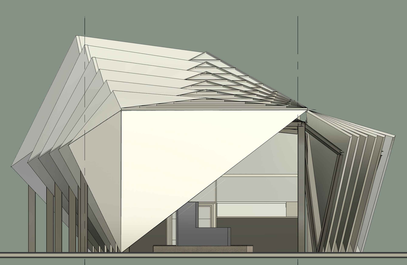

ФАСАД В ОСЯХ А-Е М1:150

ФАСАД В ОСЯХ Е-А М1:150

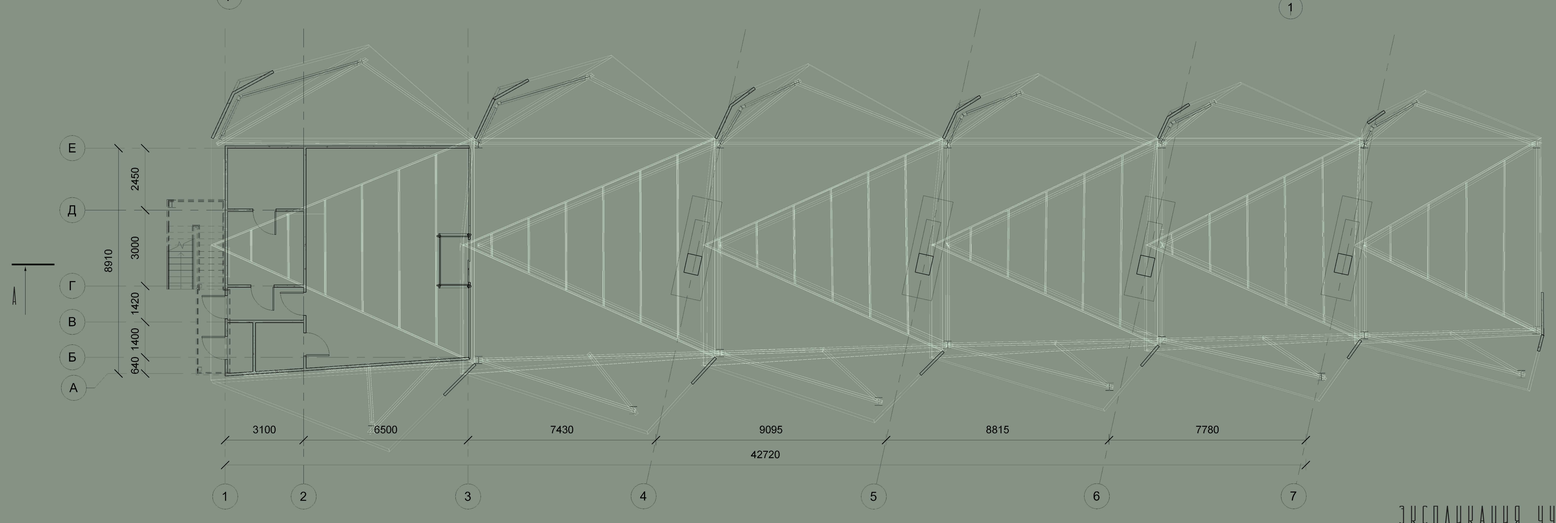

ПЛАН НА ОТМЕТКЕ +1.300 М1:150

ЭКСПЛИКАЦИЯ ПОМЕЩЕНИЙ

1	Кассовая зона	52 м²
2	Санузел	4 м²
3	Электрощитовая	2 м²
4	Коридор	4 м²
5	Склад продовольственных товаров	9 м²
6	Склад непродовольственных товаров	7 м²
7	Помещение	2 м²
8	Коридор	4 м²
9	Санузел для персонала	6 м²
10	Комната отдыха	7 м²
11	Кабинет	7 м²

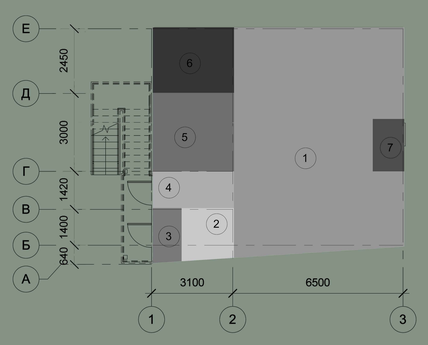

ЭКСПЛИКАЦИЯ НА ОТМЕТКЕ +0.000

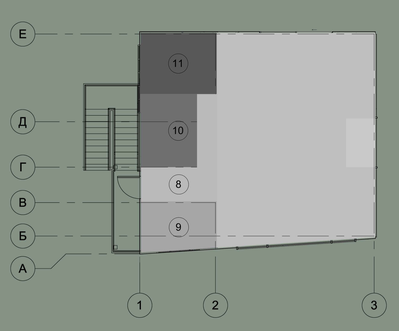

ЭКСПЛИКАЦИЯ НА ОТМЕТКЕ +0.3000 М1:

ЭКСПЛИКАЦИЯ УЧАСТКА

1	Парковочные места
2	Резервуарный парк
3	Операторная
4	Навес над ТРК
5	Площада для автоцистерны
6	Флагштоки
7	Ценовая стела

СИТУАЦИЯ М1:10000

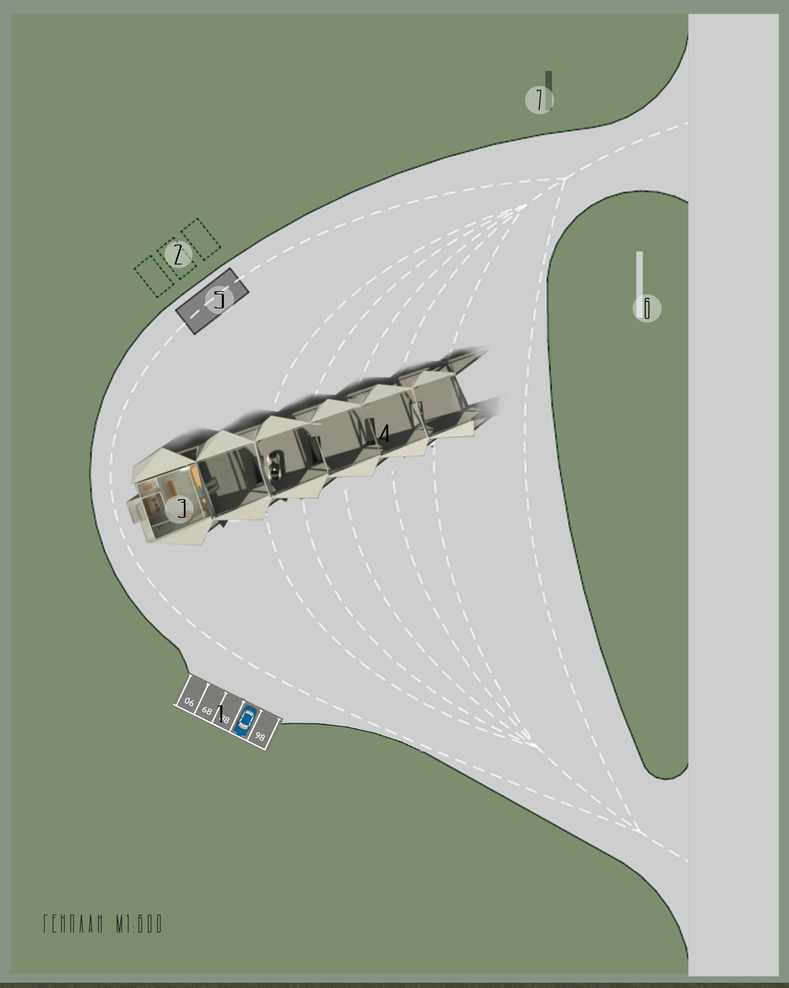

ГЕНПЛАН М1:000

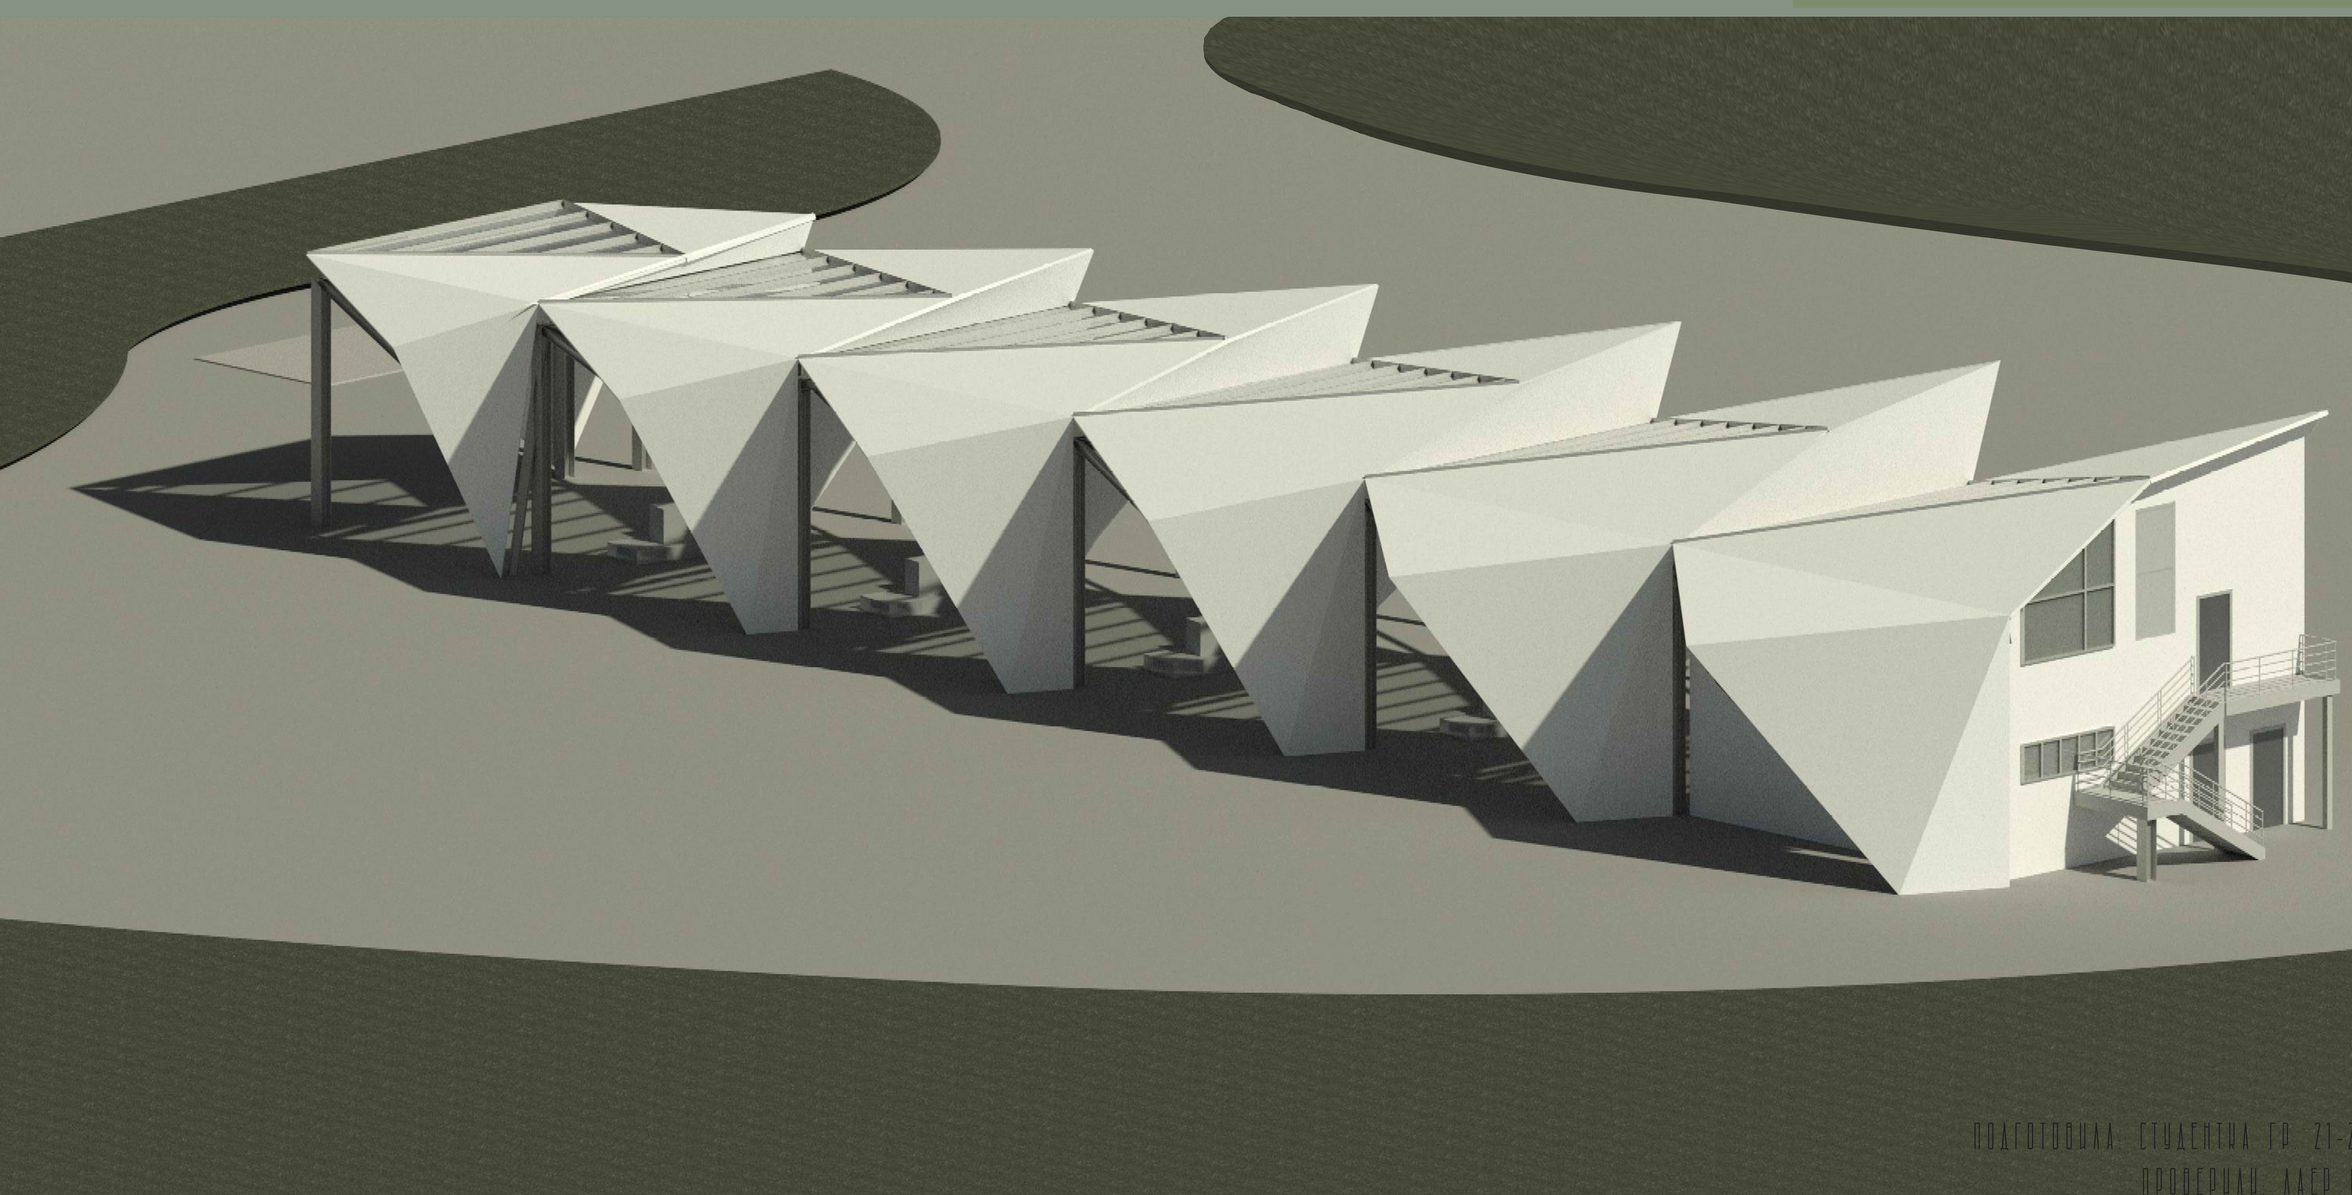

ПОДГОТОВИЛА: СТУДЕНТКА ГР. 21-214-1 ТИАЧУК А.Ю.
ПРОВЕРИЛИ: ЛАЕР С.О., ТИМАНЮК Т.Г.