

МИНИСТЕРСТВО НАУКИ И ВЫСШЕГО ОБРАЗОВАНИЯ РОССИЙСКОЙ ФЕДЕРАЦИИ
федеральное государственное бюджетное образовательное учреждение
высшего образования
«НОВОСИБИРСКИЙ ГОСУДАРСТВЕННЫЙ УНИВЕРСИТЕТ
АРХИТЕКТУРЫ, ДИЗАЙНА И ИСКУССТВ»
(НГУАДИ)

Кафедра Архитектуры

Объект: «Малоэтажный многоквартирный дом»

ПРОЕКТНАЯ ДОКУМЕНТАЦИЯ

**Раздел 2. Схема планировочной организации земельного
участка.**

ПЗУ

Выполнила: Ткачук А. Ю
гр. 21-414-1
Проверила: Свешникова О.Б.

												2	
Обозначение						Наименование						Примечание	
21-414-1-ПЗУ						Содержание тома 2						Стр.2	
21-414-1-СП						Состав проектной документации						Стр.4	
21-414-1-ПЗУ.ТЧ						Текстовая часть						Стр.6	
						а) Характеристика земельного участка, предоставленного для размещения объекта капитального строительства							
						а1) Сведения о наличии зон с особыми условиями использования территорий в пределах границ земельного участка						Стр.12	
						б) Обоснование границ санитарно-защитных зон объектов капитального строительства в пределах границ земельного участка						Стр.13	
						в) Обоснование и описание планировочной организации земельного участка в соответствии с градостроительным и техническим регламентами либо документами об использовании земельного участка						Стр.14	
						г) Техничко-экономические показатели земельного участка, предоставленного для размещения объекта капитального строительства						Стр.15	
						г) Техничко-экономические показатели земельного участка, предоставленного для размещения объекта капитального строительства							
						д) Обоснование и описание решений по инженерной подготовке территории, в том числе решений по инженерной защите территории и объектов капитального строительства от последствий опасных геологических процессов, паводковых, поверхностных и грунтовых вод							
						е) Описание организации рельефа вертикальной планировкой							
						ж) Описание решений по благоустройству территории							
						з) Обоснование зонирования территории земельного участка, предназначенного для размещения объекта капитального строительства, а также принципиальная схема размещения территориальных зон с указанием сведений о расстояниях до ближайших установленных территориальных							
</													

						3											
						зон и мест размещения существующих и проектируемых зданий, строений и сооружений (основного, вспомогательного, подсобного, складского и обслуживающего назначения) объектов капитального строительства - для объектов производственного назначения											
						и) Обоснование схем транспортных коммуникаций, обеспечивающих внешние и внутренние (в том числе межцеховые) грузоперевозки - для объектов производственного назначения											
						к) Характеристика и технические показатели транспортных коммуникаций - для объектов производственного назначения											
						л) Обоснование схем транспортных коммуникаций, обеспечивающих внешний и внутренний подъезд к объекту капитального строительства, - для объектов непроизводственного назначения											
21-414-1-ПЗУ.ГЧ						Графическая часть											
						Ситуационная схема Схема планировочной организации земельного участка											
						План благоустройства территории											
Инв. № подл.						Подп. и дата						Взам. Инв. №					

Состав проектной документации

Номер тома	Обозначение	Наименование	Примечание
1	21-414-1-ПЗУ	Раздел 2. Схема планировочной организации земельного участка	
2	21-414-1-АР	Раздел 3. Объёмно-планировочные и архитектурные решения	

Согласовано:			

Взам. Инв. №	
--------------	--

Подп. и дата	
--------------	--

Инв. № подл.	
--------------	--

						21-414-1-СП			
Изм.	Кол.уч.	Лист	№ док.	Подп.	Дата	Состав проектной документации	Стадия	Лист	Листов
Разраб.		Ткачук					П		2
							НГУАДИ		

Схема планировочной организации земельного участка

а) Характеристика земельного участка, предоставленного для размещения объекта капитального строительства

Земельный участок, отведенный под проектирование расположен в Октябрьском районе города Новосибирска.

Площадь земельного участка составляет 0,85 га.

а1) Сведения о наличии зон с особыми условиями использования территорий в пределах границ земельного участка

Отсутствуют

б) Обоснование границ санитарно-защитных зон объектов капитального строительства в пределах границ земельного участка

Не имеется

в) Обоснование и описание планировочной организации земельного участка в соответствии с градостроительным и техническим регламентами либо документами об использовании земельного участка

По Правилам землепользования и застройки города Новосибирска, утверждённым решением Совета депутатов города Новосибирска от 24.06.2009 № 1288 «О правилах землепользования и застройки города Новосибирска», участок относится к территориальной зоне застройки Ж-7 - зона застройки индивидуальными и малоэтажными жилыми домами (до 4 этажей, включая мансардный)

Предельные размеры земельных участков и предельные параметры разрешенного строительства, реконструкции объектов капитального строительства:

Предельный минимальный размер земельного участка с видом разрешенного использования "малоэтажная многоквартирная жилая застройка", "административные здания организаций, обеспечивающих предоставление коммунальных услуг", "дома социального обслуживания", "оказание социальной помощи населению", "обеспечение занятий спортом в помещениях", "магазины" - 0,1 га; (в ред. решения Совета депутатов г. Новосибирска от 27.03.2024 N 670)

Предельное максимальное количество надземных этажей зданий, строений, сооружений с иным видом разрешенного использования - 4 этажа;

Минимальный отступ от границ земельного участка - 3 м (для проекций балконов, крылец, прямков, хозяйственных построек, подземных частей объектов - 1 м).

Максимальный процент застройки в границах земельного участка для объектов капитального строительства с видом разрешенного использования "малоэтажные многоквартирные дома" - 40% (без учета эксплуатируемой кровли подземных, подвальных, цокольных частей объектов);

Изн. № подл.	Подп. и дата	Взам. Изн. №	Предельное максимальное количество надземных этажей зданий, строений, сооружений с иным видом разрешенного использования - 4 этажа; Минимальный отступ от границ земельного участка - 3 м (для проекций балконов, крылец, примыков, хозяйственных построек, подземных частей объектов - 1 м). Максимальный процент застройки в границах земельного участка для объектов капитального строительства с видом разрешенного использования "малоэтажные многоквартирные дома" - 40% (без учета эксплуатируемой кровли подземных, подвальных, цокольных частей объектов);					
							Текстовая часть	Лист
Изм.	Кол.уч.	Лист	№ док.	Подп.	Дата	2		

Предельное минимальное количество машино-мест для стоянок индивидуальных транспортных средств для объектов капитального строительства с видом разрешенного использования "малоэтажный многоквартирный дом" - 1 машино-место на 105 кв. метров площади квартир (за исключением лоджий, балконов, веранд, террас, холодных кладовых и тамбуров), но не менее 0,5 машино-места на 1 квартиру, из них не более 15% гостевых машино-мест.

По проекту отступ от границ земельного участка до границ застройки составляет 10 м.

Предельное максимальное количество надземных этажей зданий, строений, сооружений - 4 этажа, включая мансардный.

Максимальная этажность зданий в проекте 4 этажа.

Минимальный процент застройки в границах земельного участка для объектов капитального строительства в зоне застройки малоэтажными многоквартирными жилыми домами – 10%

Процент застройки земельного участка по проекту составляет 20%.

В отношении данного участка действует проект планировки, утвержденный постановлением мэрии города Новосибирска №3274 от 27.10.2020 О проведении общественных обсуждений по проекту постановления мэрии города Новосибирска «О проекте планировки и проектах межевания территории восточной части Октябрьского района».

В соответствии с СП 158.13330.2014 был произведен расчёт автостоянок: 1 машино-место на 105 кв. метров общей площади квартир, но не менее 0,5 машино-места на 1 квартиру, из них не более 15% гостевых машино-мест.

Расчет машино-мест для одного дома: $2845 \text{ м}^2 / 105 = 27$ шт.

Для двух домов на участке требуется разместить 54 машино-места.

Из них 12 м/мест, включая 4 специальных м/места парковке, открытые, а 42 м/места в подземной парковке размером 24х40 м

г) Техничко-экономические показатели земельного участка, предоставленного для размещения объекта капитального строительства

Кадастровый номер 54:35:072147

Площадь участка - 8500 м^2

Общая площадь помещений – 2845 м^2

Площадь квартир 2075 м^2

Общий строительный объем здания – 11740 м^3

Площадь застройки – 1680 м^2

Коэффициент застройки:

Коэффициент плотности застройки:

$$K_z = S_{\text{застр}} / S_{\text{терр}},$$

$$K_z = 2\%$$

$$K_{\text{пл.з.}} = S_{\text{эт}} / S_{\text{терр}},$$

$$K_z = 3\%$$

Плотность застройки:

Инв. № подл.	Подп. и дата	Взам. Инв. №	Текстовая часть						Лист
									3
Изм.	Кол.уч.	Лист	№ док.	Подп.	Дата				

Объект непроизводственного назначения

к) Характеристика и технические показатели транспортных коммуникаций (при наличии таких коммуникаций) - для объектов производственного назначения

Объект непроизводственного назначения.

л) Обоснование схем транспортных коммуникаций, обеспечивающих внешний и внутренний подъезд к объекту капитального строительства

Подъезд к проектируемым жилым домам решен с улиц Рябиновой и Выборной.

По проектируемым внутриплощадочным проездам предусмотрена возможность проезда всех категорий автотранспорта, в том числе пожарной спецтехники.

Движение пожарных машин возможно, как с использованием проездов, так и тротуарной части проектируемой застройки.

Инв. № подл.	Подп. и дата	Взам. Инв. №						
						Текстовая часть	Лист	
							5	
Изм.	Кол.уч.	Лист	№ док.	Подп.	Дата			

Экспликация зданий и сооружений

Номер на плане	Наименование	Примечание
1	Малоэтажный многоквартирный дом 1	
2	Малоэтажный многоквартирный дом 2	
3	Крытый въезд в подземную парковку	

Ведомость тротуаров, дорожек и покрытий

Поз	Наименование	Тип	Площадь покрытия, м2	Примечание
1	Проезды и парковки с асфальтобетонным покрытием		991	
2	Покрытие детских площадок		987	
3	Тротуары и площадки с покрытием тротуарной плитки		660	
4	Укрепленные проезды		520	


Условные обозначения:

- 1

Номер здания
- Красные линии
- Границы участка
- Границы подземной парковки

Условные изображение типов покрытия:

- Проезды и площадки с покрытием из асфальтабетона
- Площадки с резиновым покрытием
- Площадки и тротуары с покрытием из тротуарной плитки с возможностью проезда
- Газон укрепленный
- Газон обыкновенный

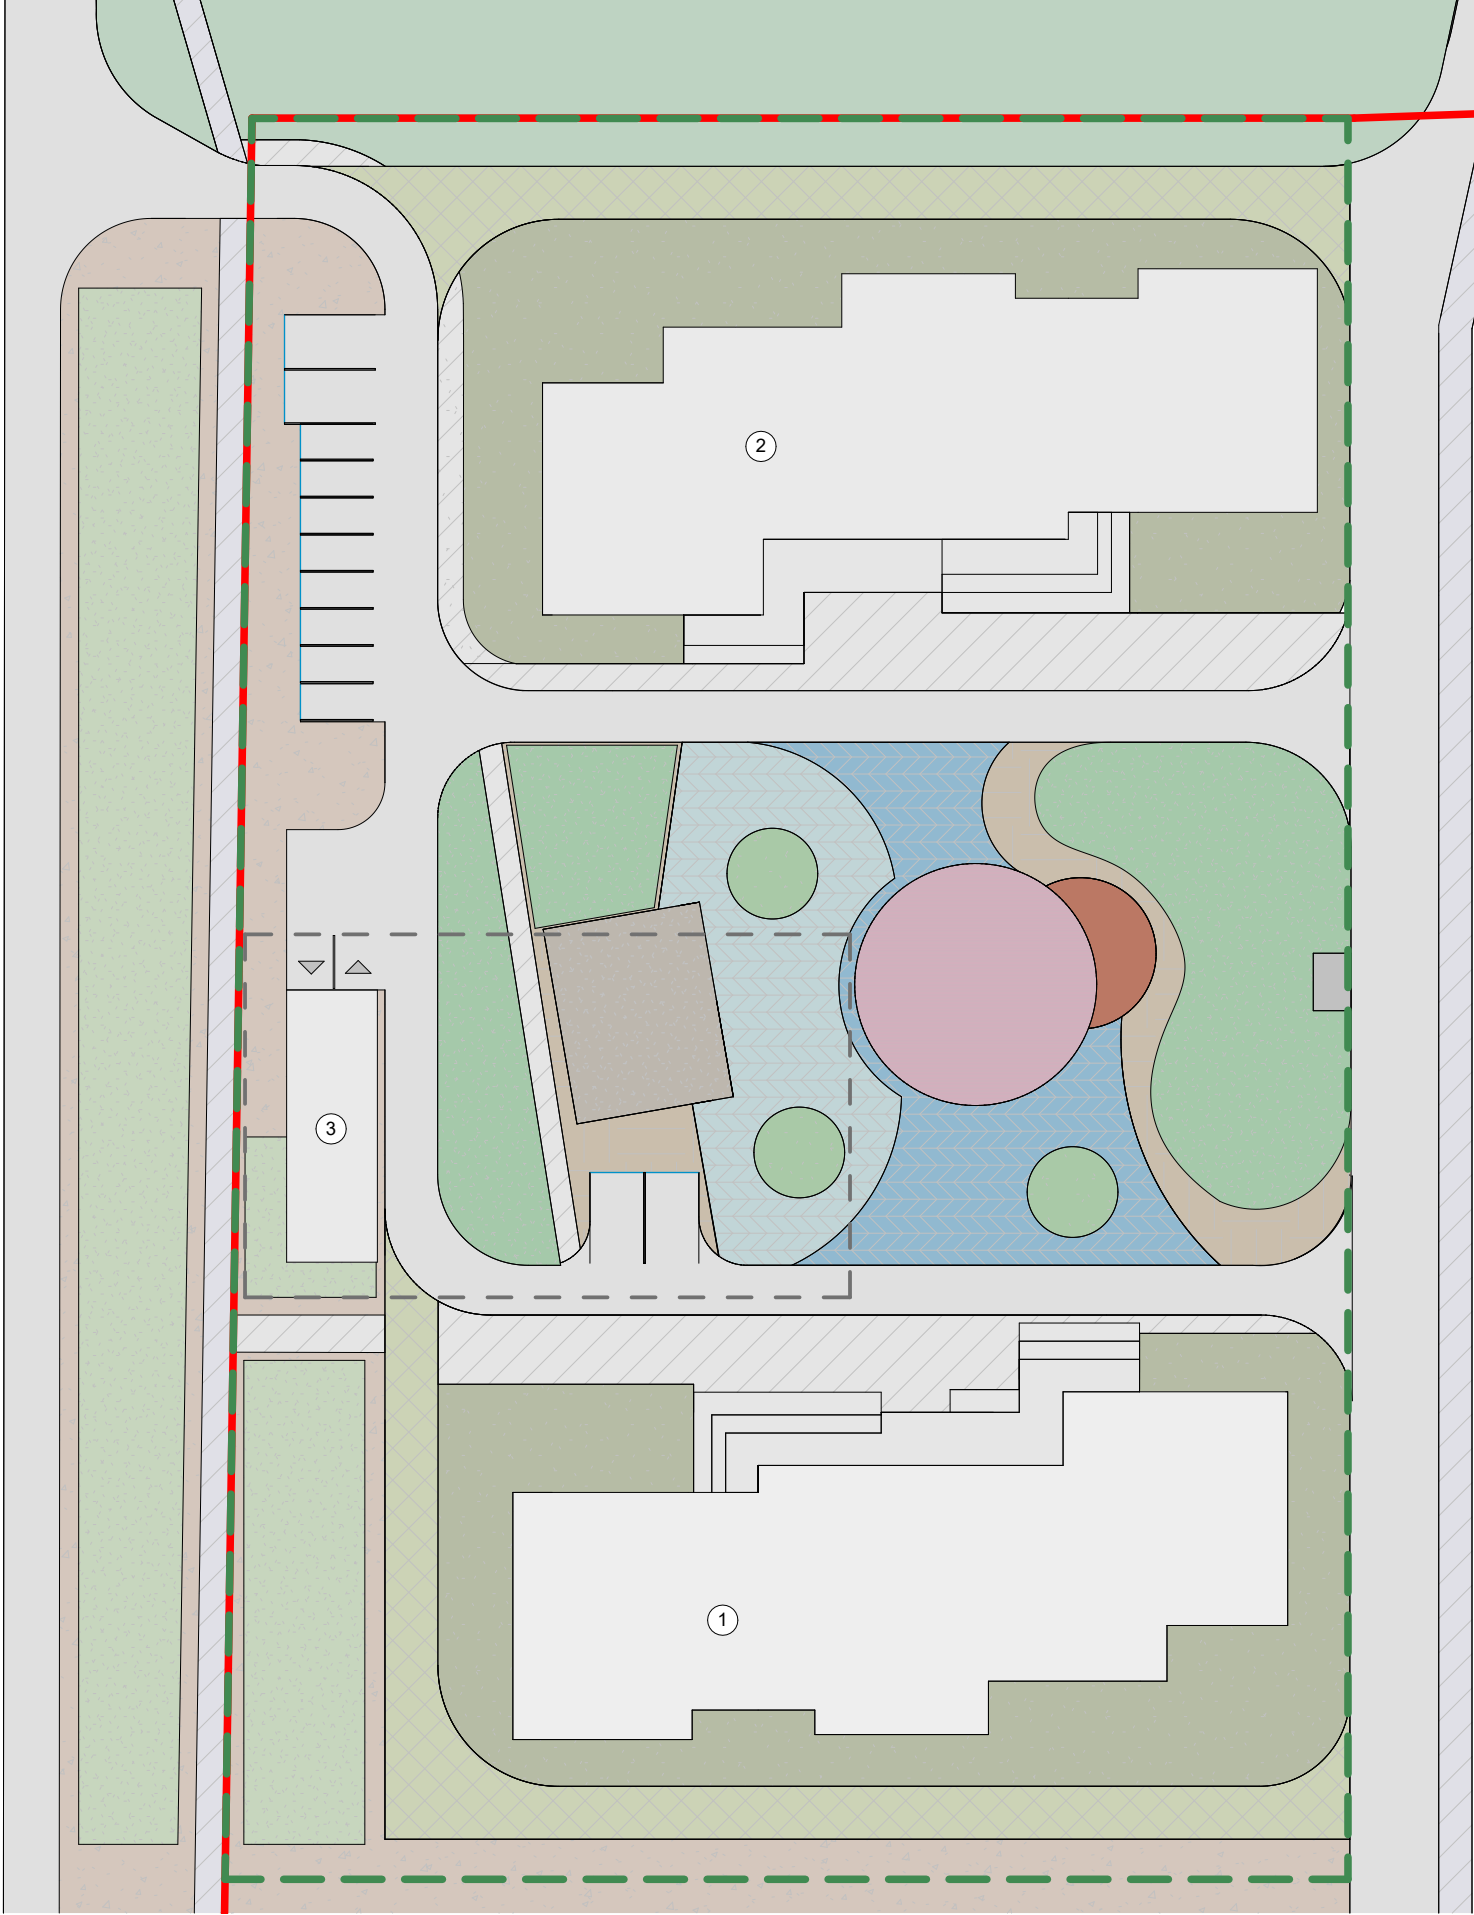

						21-414-1 ПЗУ.ГЧ			
						Малозэтажный многоквартирный дом на ул. Рябиновая			
Изм.	Кол. уч.	Лист	№ док.	Подпись	Дата	Малозэтажный многоквартирный дом	Стадия	Лист	Листов
Разработала	Ткачук А.Ю.						П	2	2
							Схема планировочной организации участка	НГУАДИ	